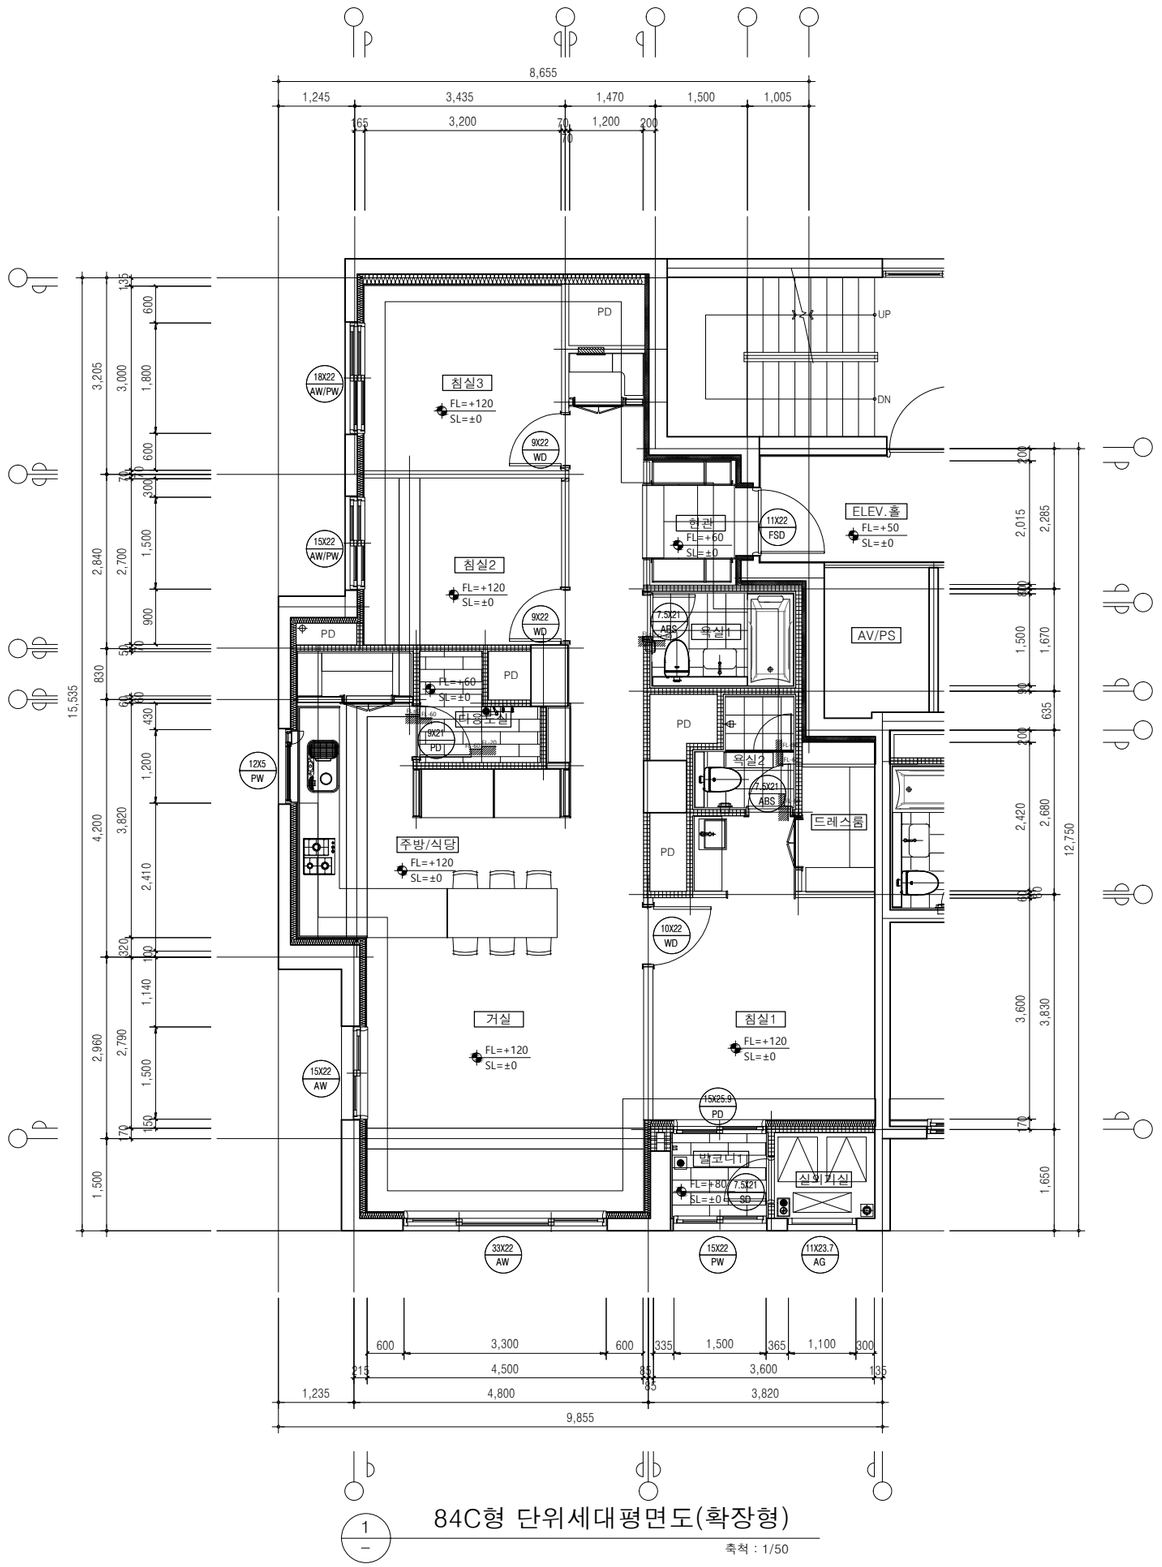


1
–

84C형 단위세대평면도(확장형)

축척 : 1/50

CLIENT

방배5구역 주택재건축정비사업조합

93, Dogu-ro, Seocho-gu, Seoul, Korea, 06675. www.bb5.kr

ARCHITECT

SAMOO ARCHITECTS & ENGINEERS

1077, Cheonho-daero, Gangdong-gu, Seoul Korea, 05340. www.samoo.com

STRUCTURAL CONSULTANTS
(주)경재구조엔지니어링
T:02-413-3190

MECHANICAL CONSULTANTS
(주)일송엔지니어링 기술사사무소
T:02-549-3840

ELECTRICAL CONSULTANTS
(주)하예성엔지니어링
T:02-2026-5435-7

CIVIL ENGINEERS
(주)인아엔지니어링
T:02-2203-4132

LANDSCAPE DESIGNERS
(주)씨에이조경기술사사무소
T:02-543-4454

LANDSCAPE DESIGNERS
(주)그룹한 어소시에이트
T:02-521-1122

NOTES

0. 면적변경,구조변경 또는 관례법령 저촉사항 등이 아닌 세대 내부 인테리어에 대한 사항은 변경될 수 있음.
1. 건본주택과 설계도면이 상이한 경우 건본주택을 우선
2. 외부창호는 내풍압 구조검토결과에 따라 세대별로 다르게 시공될 수 있음
3. 수전의 위치는 실시공시 다르게 시공될 수 있음
4. 세대내 창호의 개폐방향및 손잡이 위치는 실시공시 변경될 수 있음
5. 선홈통의 개소와 위치는 실시공시 변경될 수 있음
6. 수전이 없는(물을사용하지 않는)발코니는 배수설비가 설치되지 않음
7. 단위세대 평면도와 타도면과의 상이한 부분은 단위세대 평면도를 우선함. 단, 단열마감은 단열계획도를 우선
8. 고정형이 아닌 가구, 기기(가전제품,식탁,의자,실외기등)와 점선표현된 가구는 시공에 포함하지 않음
9. 고정형 가구 및 거울 (현관,주방,침실,욕실, 드레스룸등)이 설치되는 곳의 바닥,벽,천장에는 마감재가 설치되지 않음
10. 내부 마감사항은 건본주택 마감기준을 우선함
11. 실내외 재료마감표와 타도면의 재료가 상이할 경우 실내,외재료 마감표를 우선함
12. 타일 나누기는 실시공시시 변경될 수 있음
13. 상하/좌우 인접세대의 확장유무에 따라 일부 발코니 벽체 마감선이 이동 될수 있음
14. 지상1층, 피로티 및 부대시설 상부층은 하향식피난시다리 미적용 (피로티 및 부대시설 상부층은 해당공간에 완강기 설치)
15. 피난시다리 위치는 현장여건에 따라 변경될 수 있음
16. 빙크대 하부/현관 신발장 하부는 판넬히팅 제외
17. 경량벽,ALC 또는 조적으로 표기된 부분은 현장시공여건에 따라 조적, 비내력콘크, 경량벽 등으로 변경시공 할 수 있음
18. PD 및 AD내벽에는 마장 없음
19. 가스쿡탑 또는 전기쿡탑의 형태는 세대별 선택 옵션에 따라 변경될
20. 커튼박스 사이즈는 현장 여건에 따라 변경시공 될 수 있음
21. 씽크대 젠다이(두겁),욕실장하부,현관디딤판 하부는 코킹 생략될 수 있음
22. 씽크대/아일랜드 상부장 측면 벽지 및 타일 마감일 경우, 코킹 생략될 수 있음
23. 화장실,다용도실 문틀 하부 재료분리대 접합부 코킹 생략될 수 있음
24. 신발장,팬트리,드레스룸 내 걸레받이 하부 코킹 생략 될 수 있음
25. 사워부스 칸막이 프레임 상부 코킹 생략될 수 있음
26. 지정마루 시공시 일부 허용오차 범위내 유격 발생할 수 있음
27. 현관 디딤판 규격은 종문 옵션에 따라 변경될 수 있음
28. 씽크대/아일랜드 싱판 하부 코킹,물끊기홈 생략될 수 있음
29. 화장실 내부 벽 타일은 천장재와 맞닿은 부위까지만 시공하며, 천장몰딩과 천장재 달대는 시공하지 않음
30. 화장실/발코니 등 구배를 요하는 바닥마감 두께는 구배에 따라 감소될 수 있음
31. 온수분배기 배관 주위는 누수여부 확인을위해 보온재 미시공
32. 물시공 발코니,유틸리티,화장실/사워부스의 바닥 마감면은 거실과 단차 발생함
33. 고정형 가구 및 거울이 설치되는 바닥,벽,천장은 마감재가 설치되지 않음
34. 주방창호 열림 방향은 우열림 기준임(대칭타입 포함)
35. ▩ : ALC블럭

REV.	DATE	DESCRIPTION	DRN	CHK	APP
4					
3					
2					
1					

PROJECT TITLE
방배5구역 주택재건축정비사업
NO. 12075

DRAWING TITLE
84C형 단위세대평면도(확장형)

CHECKED BY/ DATE	APPROVED BY/ DATE
–	차재영/24.10.
PROJECT ARCHITECT	PROJECT MANAGER
송인성	성낙경
ENGINEER	DRAWN BY/ DATE
–	–

SCALE
A1: 1/50 A3: 1/100

DRAWNG NO. A31-012 REV. 0