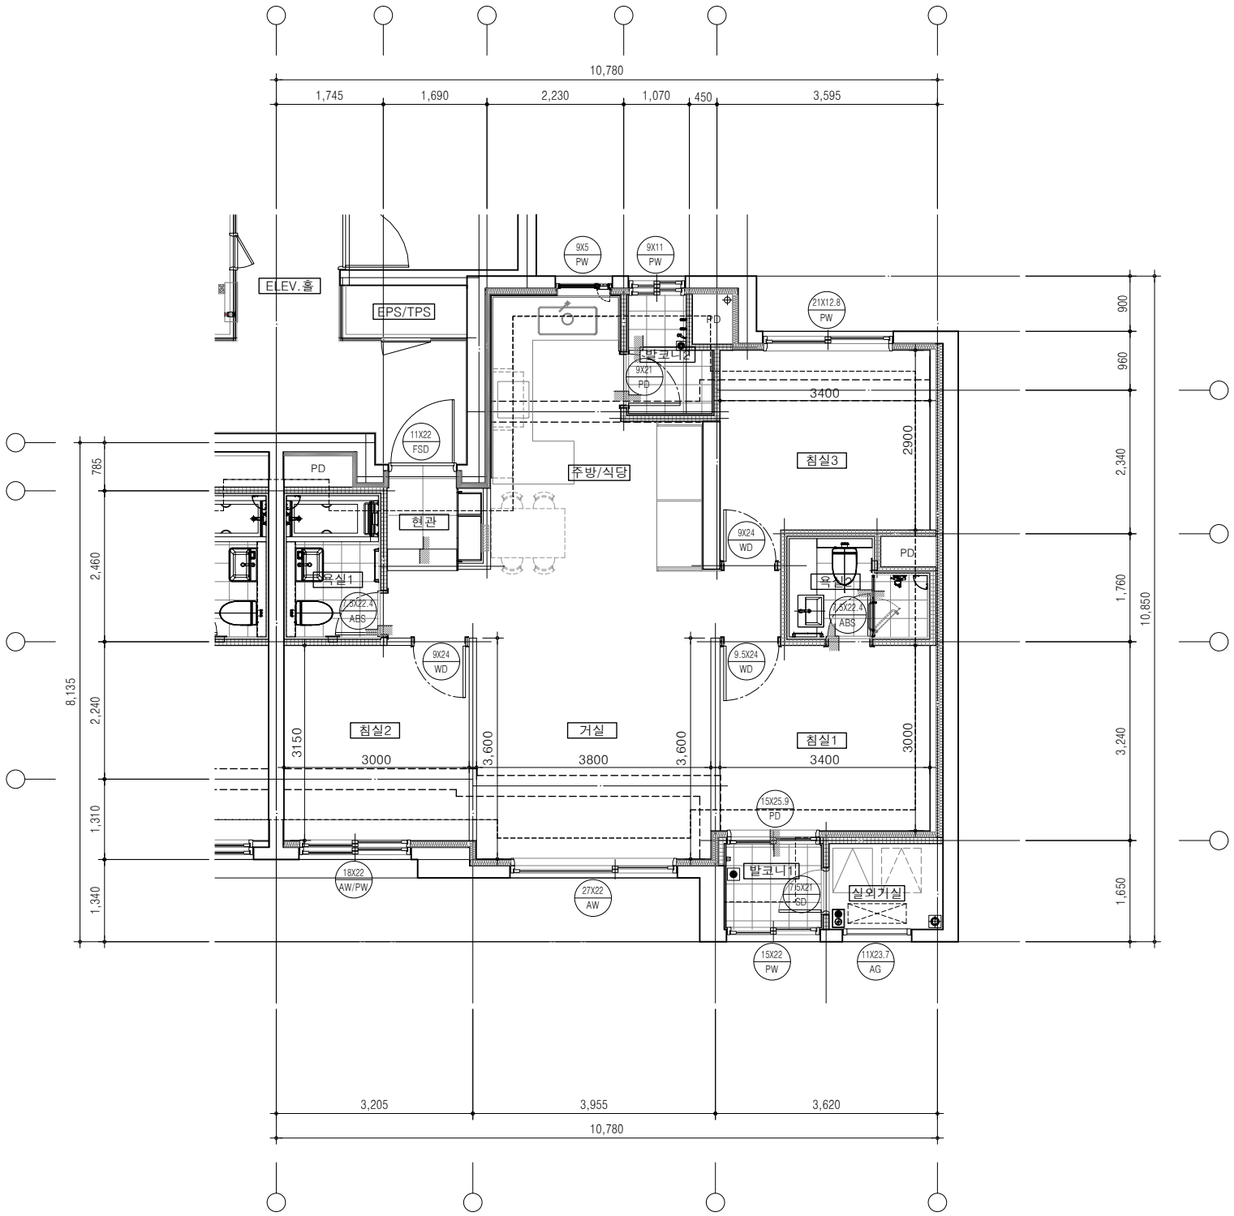


1 / – 59A형 단위세대평면도(확장형)

축척 : 1/50

CLIENT

ARCHITECT

STRUCTURAL CONSULTANTS

NOTES

- 도면상의 치수는 참고 치수 이며, 실측시 결례분이 등의 시공으로 오차가 발생할 수 있음

REV.	DATE	DESCRIPTION	DRN	CHK	APP
4					
3					
2					
1					

PROJECT TITLE

NO.

DRAWING TITLE


59A형 단위세대평면도(확장형)

CHECKED BY/ DATE	APPROVED BY/ DATE
–	–
PROJECT ARCHITECT	PROJECT MANAGER
–	–
ENGINEER	DRAWN BY/ DATE
–	–

SCALE

A1: 1/50 A3: 1/100

DRAWING NO. A31-002 REV. 0

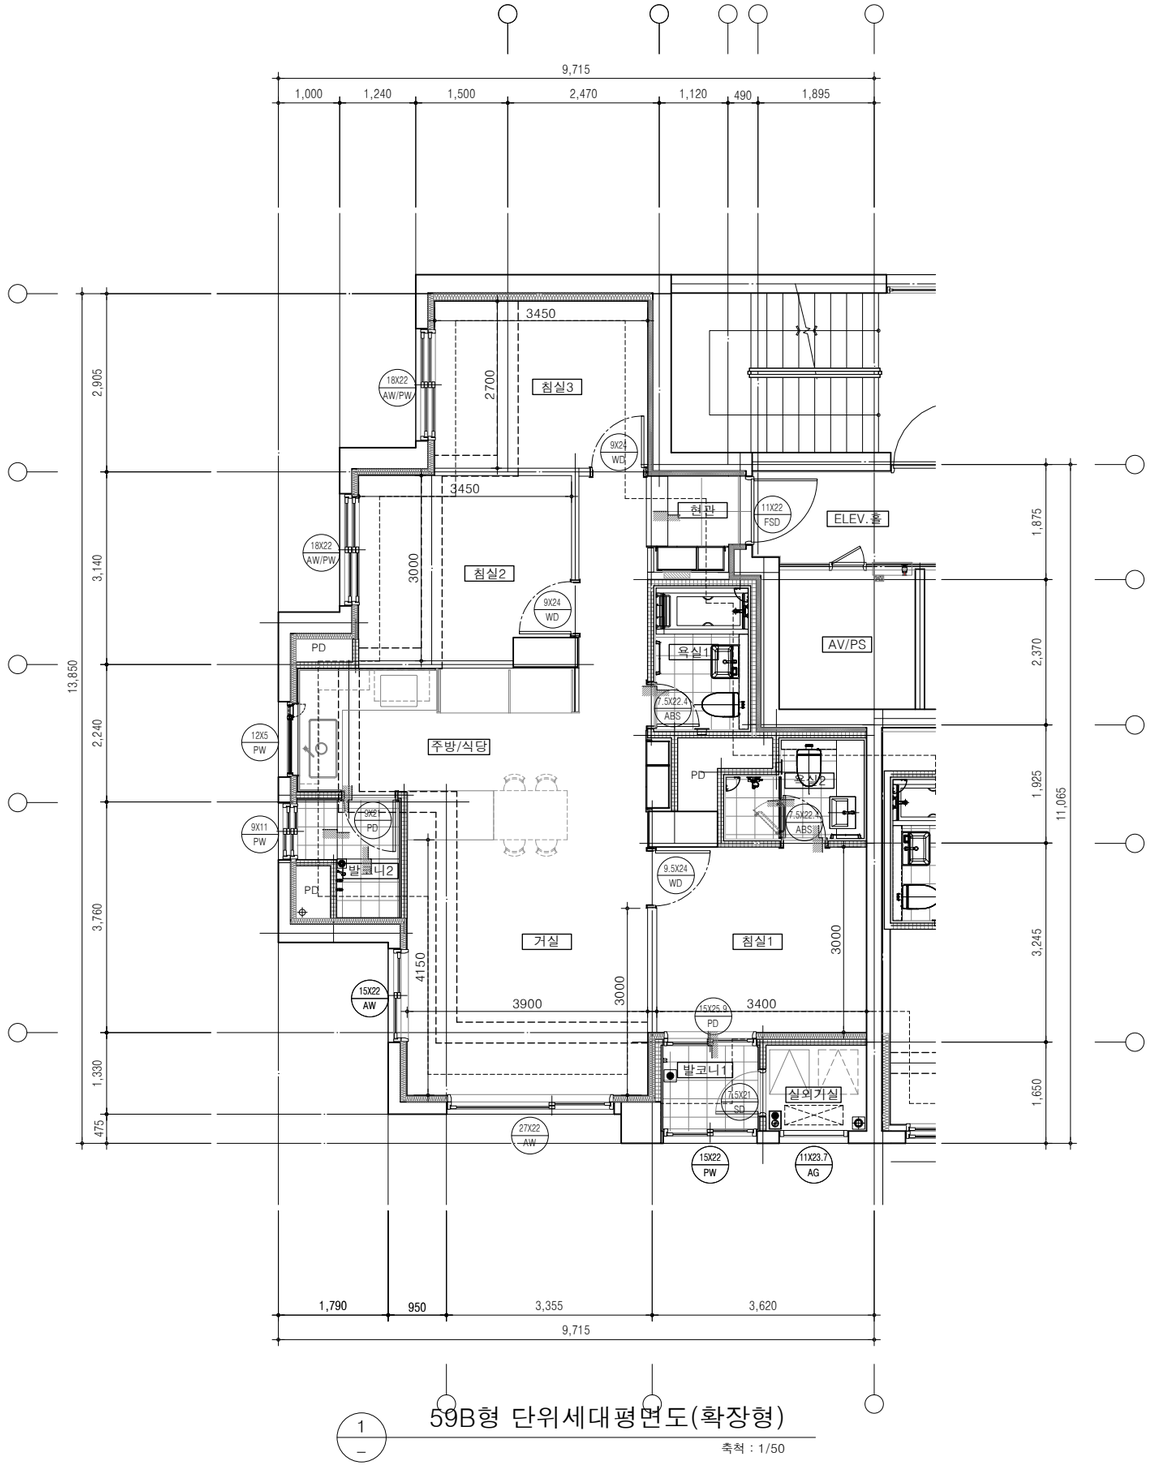

1 59B형 단위세대평면도(확장형)

축척 : 1/50

CLIENT

ARCHITECT

STRUCTURAL CONSULTANTS

NOTES

- 도면상의 치수는 참고 치수 이며, 실측시 결례받이 등의 시공으로 오차가 발생할 수 있음

REV.	DATE	DESCRIPTION	DRN	CHK	APP
4					
3					
2					
1					

PROJECT TITLE

NO.

DRAWING TITLE


59B형 단위세대평면도(확장형)

CHECKED BY/ DATE	APPROVED BY/ DATE
-	-
PROJECT ARCHITECT	PROJECT MANAGER
-	-
ENGINEER	DRAWN BY/ DATE
-	-

SCALE

A1: 1/50 A3: 1/100

DRAWING NO. A31-004 REV. 0

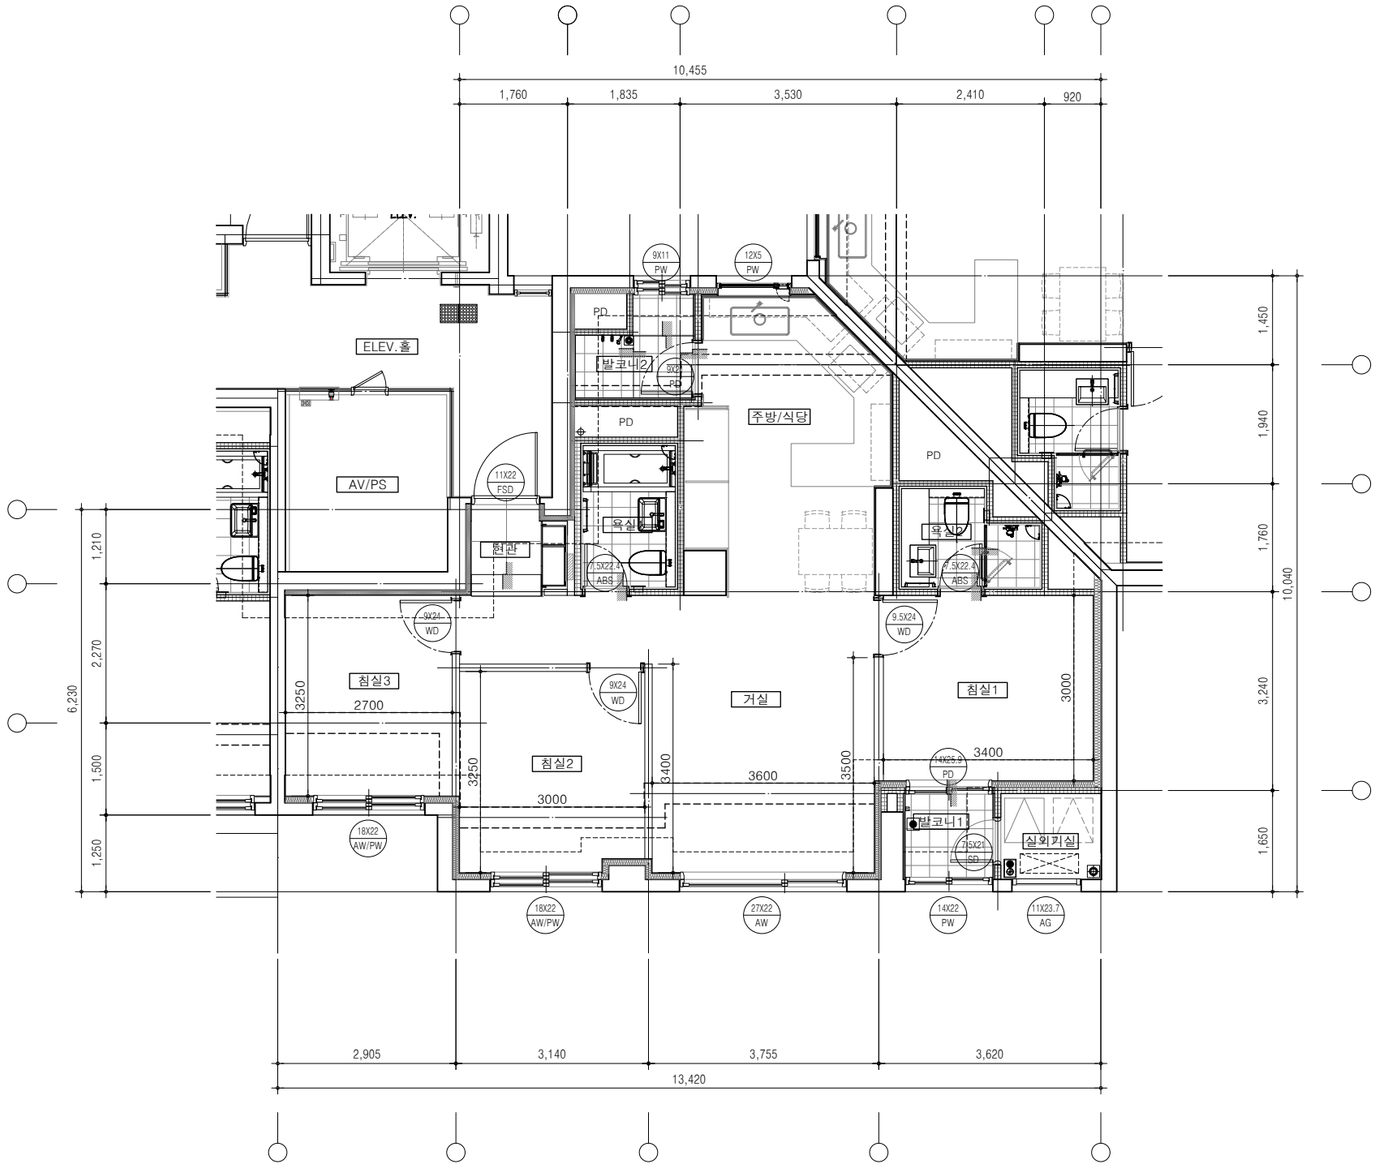

1 — 59C형 단위세대평면도(확장형)

축척 : 1/50

CLIENT

ARCHITECT

STRUCTURAL CONSULTANTS

NOTES

- 도면상의 치수는 참고 치수 이며, 실측시 결례분이 등의 시공으로 오차가 발생할 수 있음

REV.	DATE	DESCRIPTION	DRN	CHK	APP
4					
3					
2					
1					

PROJECT TITLE

NO.

DRAWING TITLE

59C형 단위세대평면도(확장형)


CHECKED BY/ DATE	APPROVED BY/ DATE
–	–
PROJECT ARCHITECT	PROJECT MANAGER
–	–
ENGINEER	DRAWN BY/ DATE
–	–

SCALE

A1: 1/50 A3: 1/100

DRAWING NO. A31-006

REV. 0

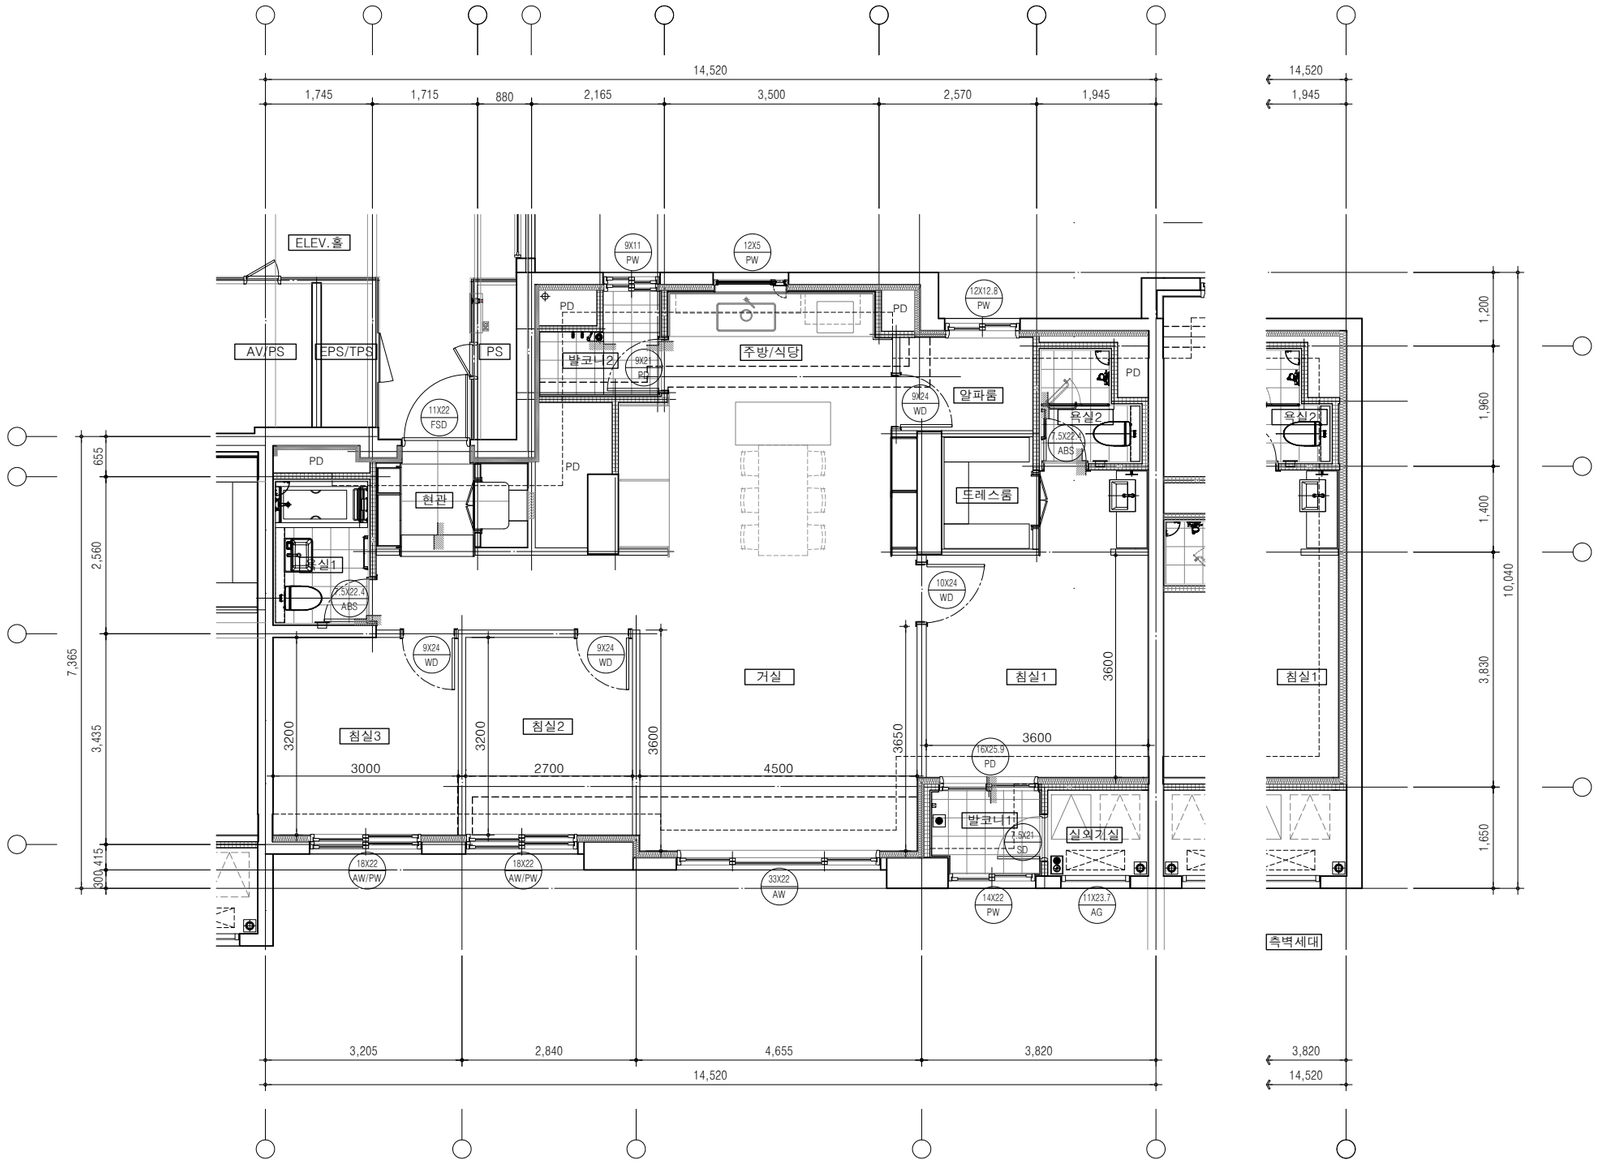

1 _ 84A형 단위세대평면도(확장형)

축척 : 1/50

CLIENT

ARCHITECT

STRUCTURAL CONSULTANTS

NOTES

- 도면상의 치수는 참고 치수 이며, 실측시 결례분이 등의 시공으로 오차가 발생할 수 있음

REV.	DATE	DESCRIPTION	DRN	CHK	APP
4					
3					
2					
1					

PROJECT TITLE

NO.

DRAWING TITLE


84A형 단위세대평면도(확장형)

CHECKED BY/ DATE	APPROVED BY/ DATE
-	-
PROJECT ARCHITECT	PROJECT MANAGER
-	-
ENGINEER	DRAWN BY/ DATE
-	-

SCALE

A1: 1/50 A3: 1/100

DRAWING NO. A31-008 REV. 0

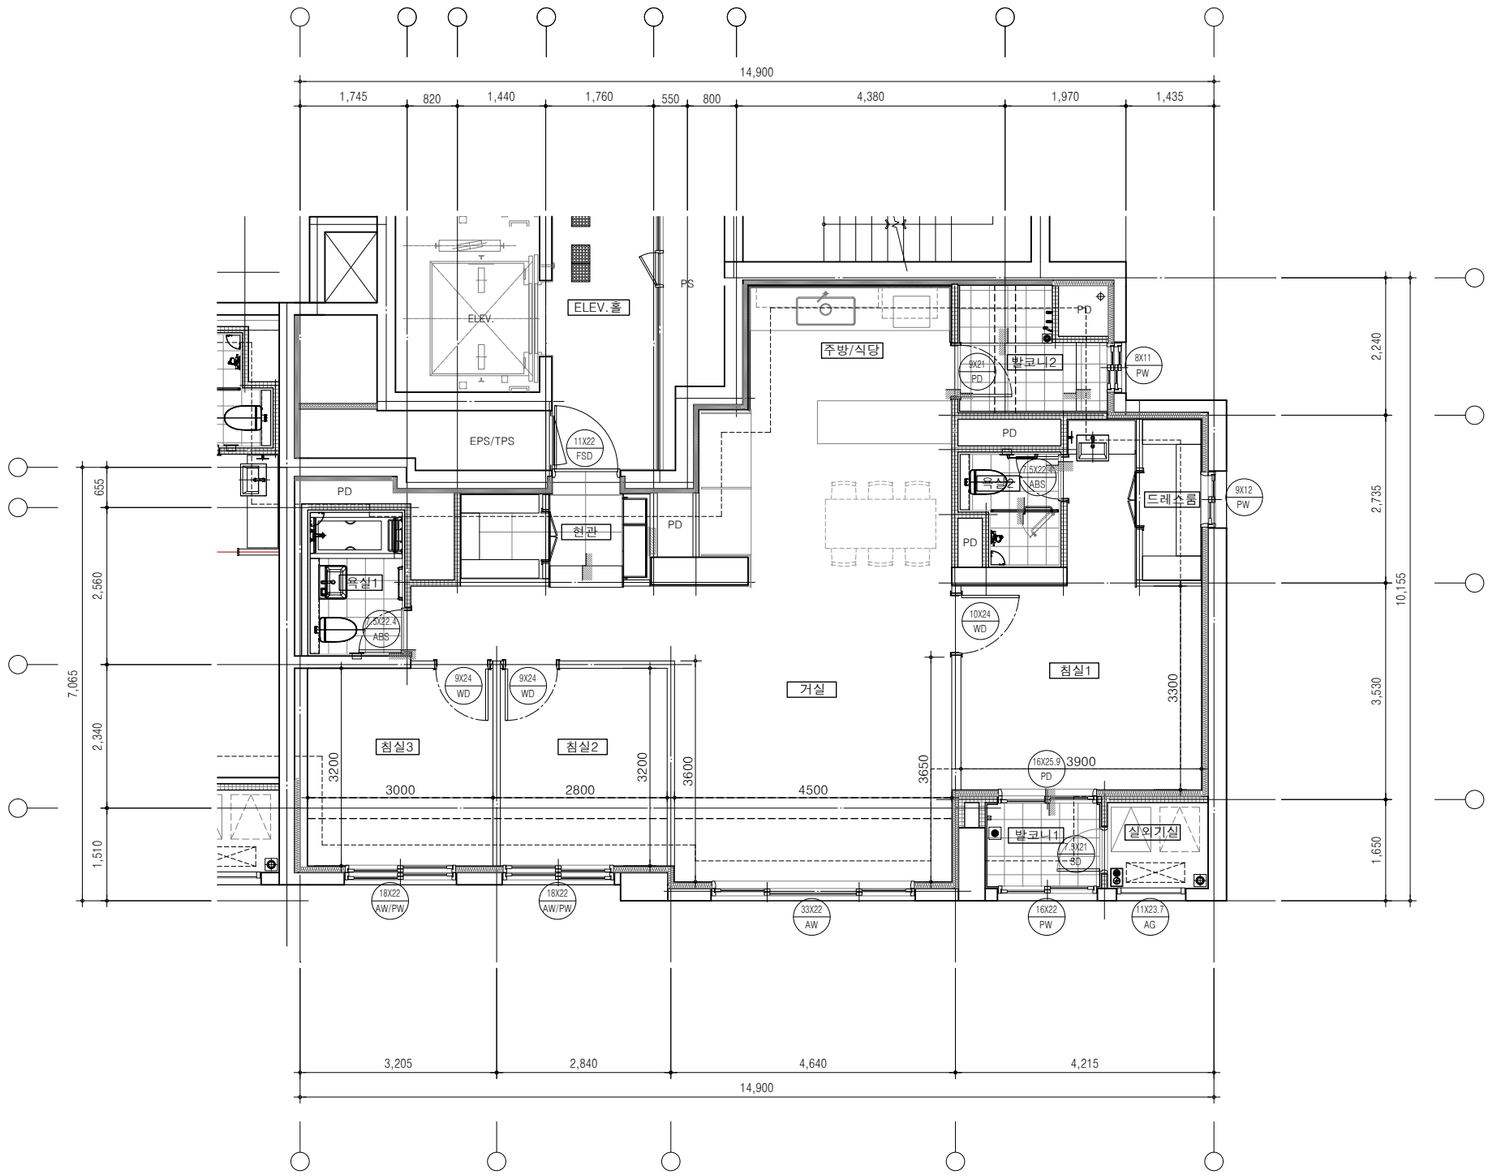

1 — 84B형 단위세대평면도(확장형)

축척 : 1/50

CLIENT

ARCHITECT

STRUCTURAL CONSULTANTS

NOTES

- 도면상의 치수는 참고 치수 이며, 실측시 결레받이 등의 시공으로 오차가 발생할 수 있음

REV.	DATE	DESCRIPTION	DRN	CHK	APP
4					
3					
2					
1					

PROJECT TITLE

NO.

DRAWING TITLE


84B형 단위세대평면도(확장형)

CHECKED BY/ DATE	APPROVED BY/ DATE
–	–
PROJECT ARCHITECT	PROJECT MANAGER
–	–
ENGINEER	DRAWN BY/ DATE
–	–

SCALE

A1: 1/50 A3: 1/100

DRAWING NO. A31-010 REV. 0

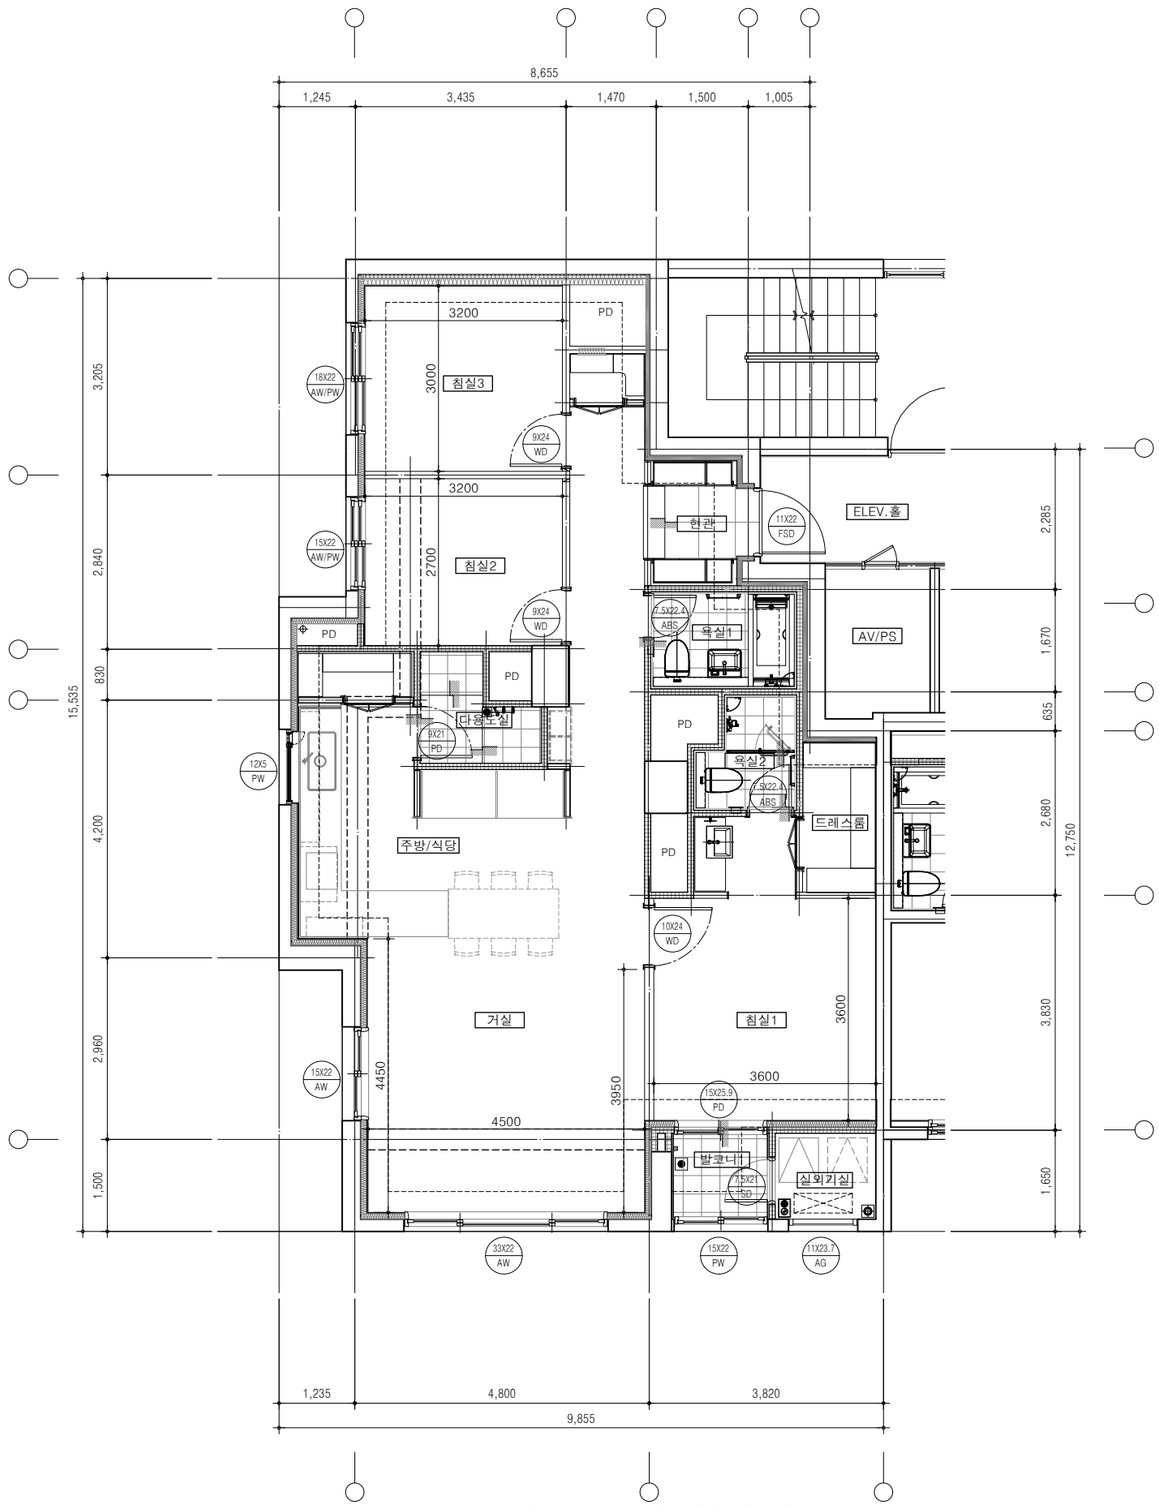

1 84C형 단위세대평면도(확장형)

축척 : 1/50

CLIENT

ARCHITECT

STRUCTURAL CONSULTANTS

NOTES

- 도면상의 치수는 참고 치수 이며, 실측시 결례분이 등의 시공으로 오차가 발생할 수 있음

REV.	DATE	DESCRIPTION	DRN	CHK	APP
4					
3					
2					
1					

PROJECT TITLE

NO.

DRAWING TITLE


84C형 단위세대평면도(확장형)

CHECKED BY/ DATE	APPROVED BY/ DATE
–	–
PROJECT ARCHITECT	PROJECT MANAGER
–	–
ENGINEER	DRAWN BY/ DATE
–	–

SCALE

A1: 1/50 A3: 1/100

DRAWING NO. A31-012 REV. 0

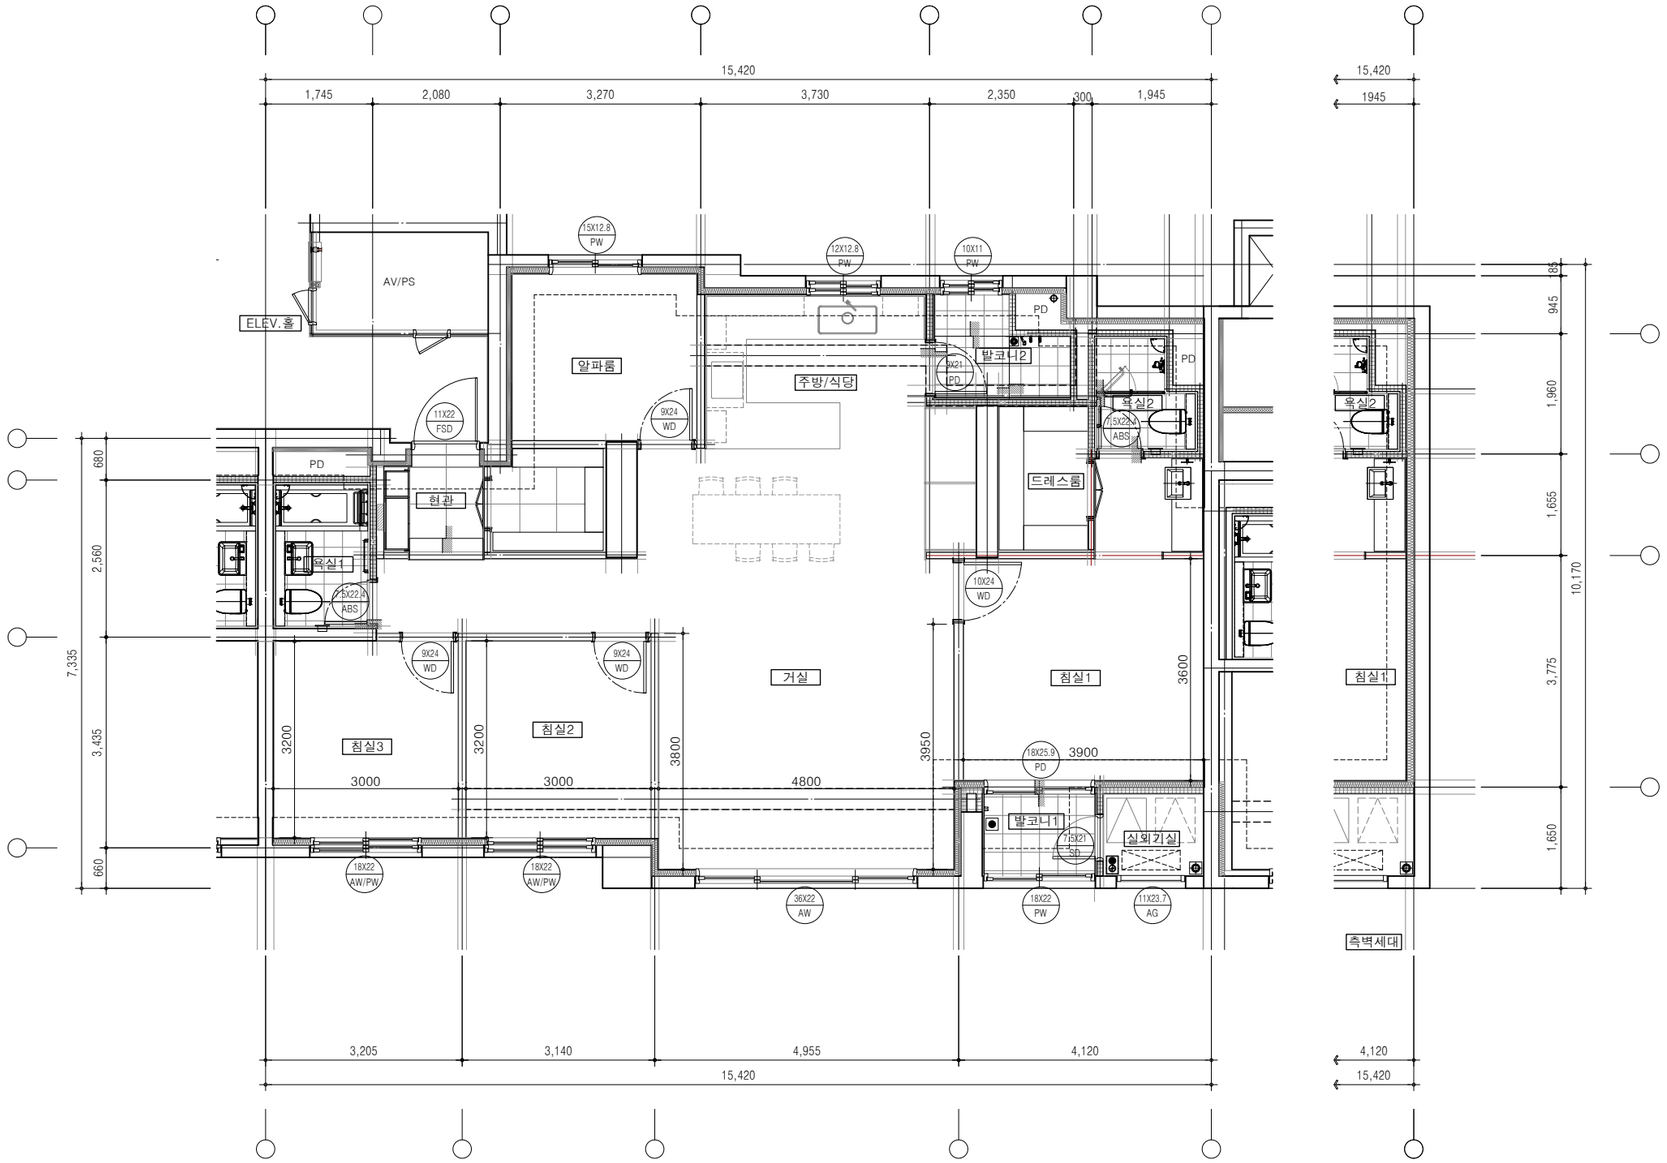

1 — 101A형 단위세대평면도(확장형)

축척 : 1/50

CLIENT

ARCHITECT

STRUCTURAL CONSULTANTS

NOTES

- 도면상의 치수는 참고 치수 이며, 실측시 결레받이 등의 시공으로 오차가 발생할 수 있음

REV.	DATE	DESCRIPTION	DRN	CHK	APP
4					
3					
2					
1					

PROJECT TITLE

NO.

DRAWING TITLE


101A형 단위세대평면도(확장형)

CHECKED BY/ DATE	APPROVED BY/ DATE
–	–
PROJECT ARCHITECT	PROJECT MANAGER
–	–
ENGINEER	DRAWN BY/ DATE
–	–

SCALE

A1: 1/50 A3: 1/100

DRAWING NO. A31-014 REV. 0

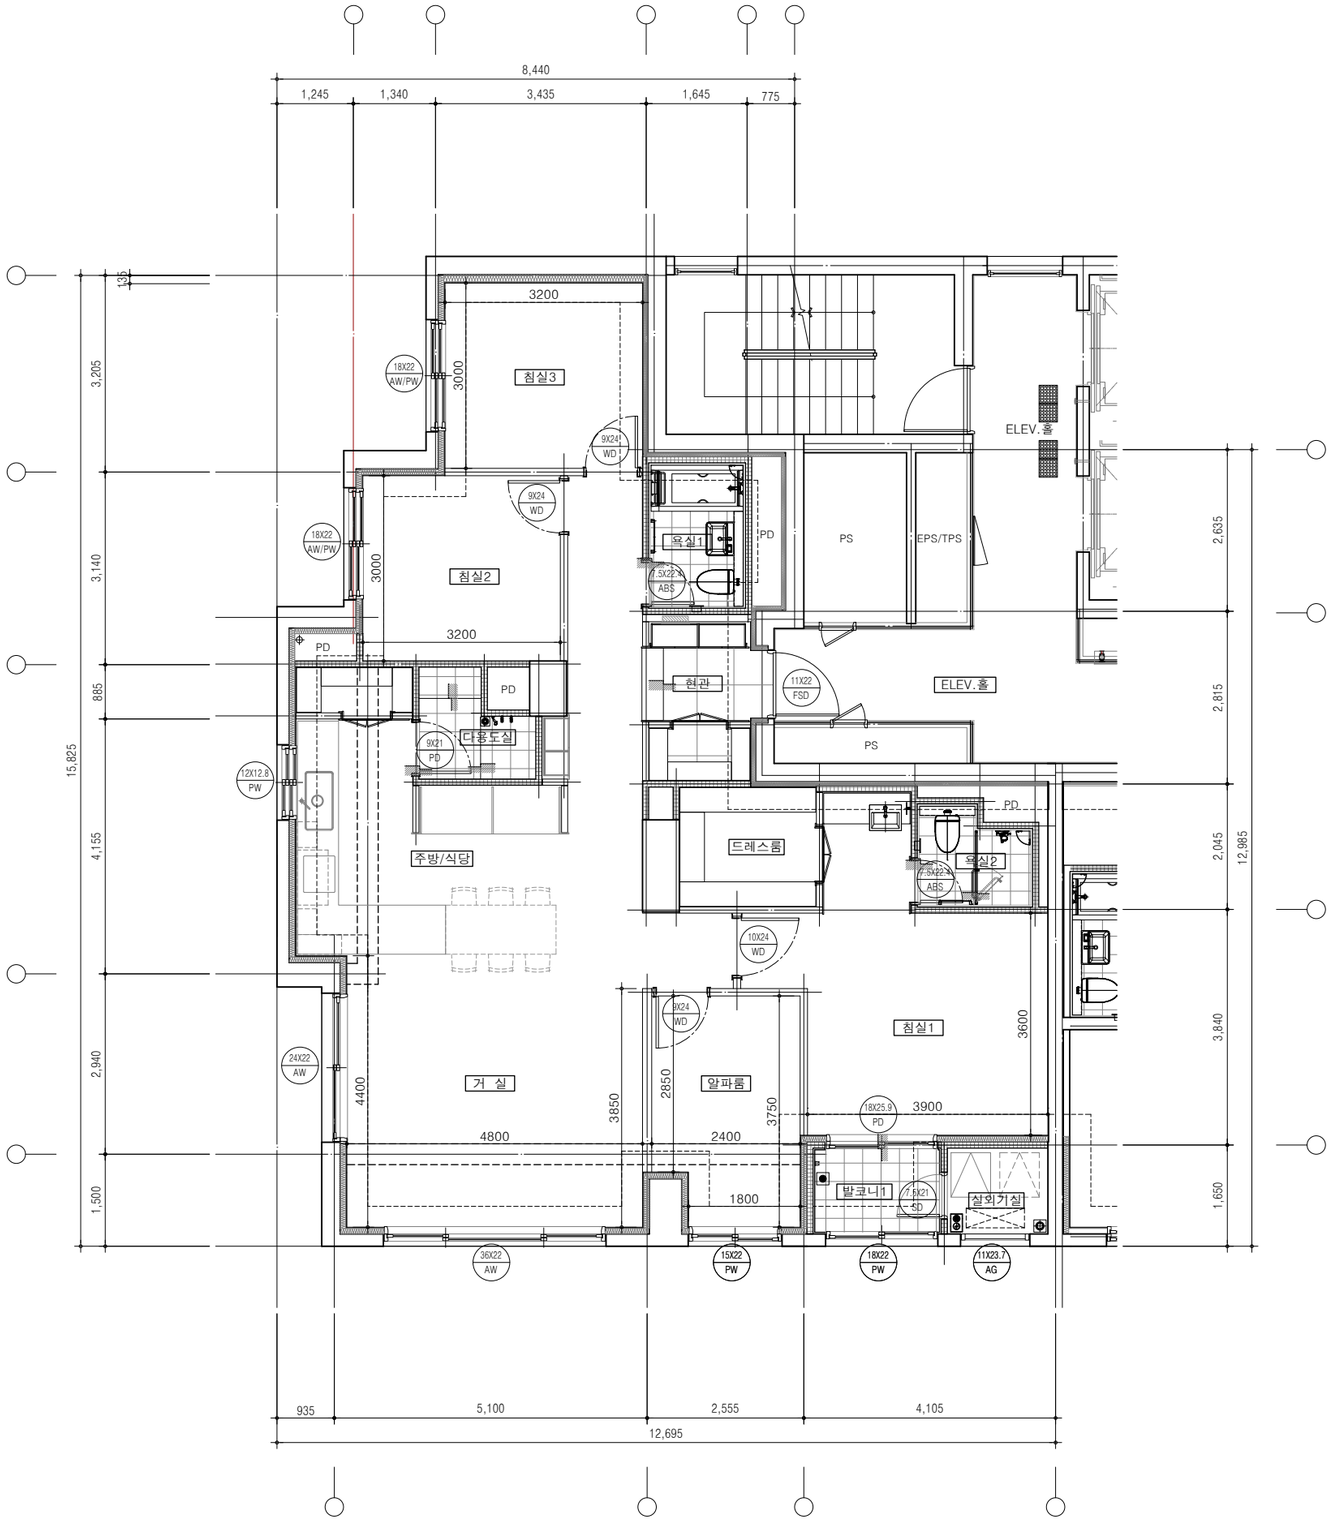

1 / – 101B형 단위세대평면도(확장형)

축척 : 1/50

CLIENT

ARCHITECT

STRUCTURAL CONSULTANTS

NOTES

- 도면상의 치수는 참고 치수 이며, 실측시 결례분이 등의 시공으로 오차가 발생할 수 있음

REV.	DATE	DESCRIPTION	DRN	CHK	APP
4					
3					
2					
1					

PROJECT TITLE

NO.

DRAWING TITLE


101B형 단위세대평면도(확장형)

CHECKED BY/ DATE	APPROVED BY/ DATE
–	–
PROJECT ARCHITECT	PROJECT MANAGER
–	–
ENGINEER	DRAWN BY/ DATE
–	–

SCALE

A1: 1/50 A3: 1/100

DRAWING NO. A31-016 REV. 0

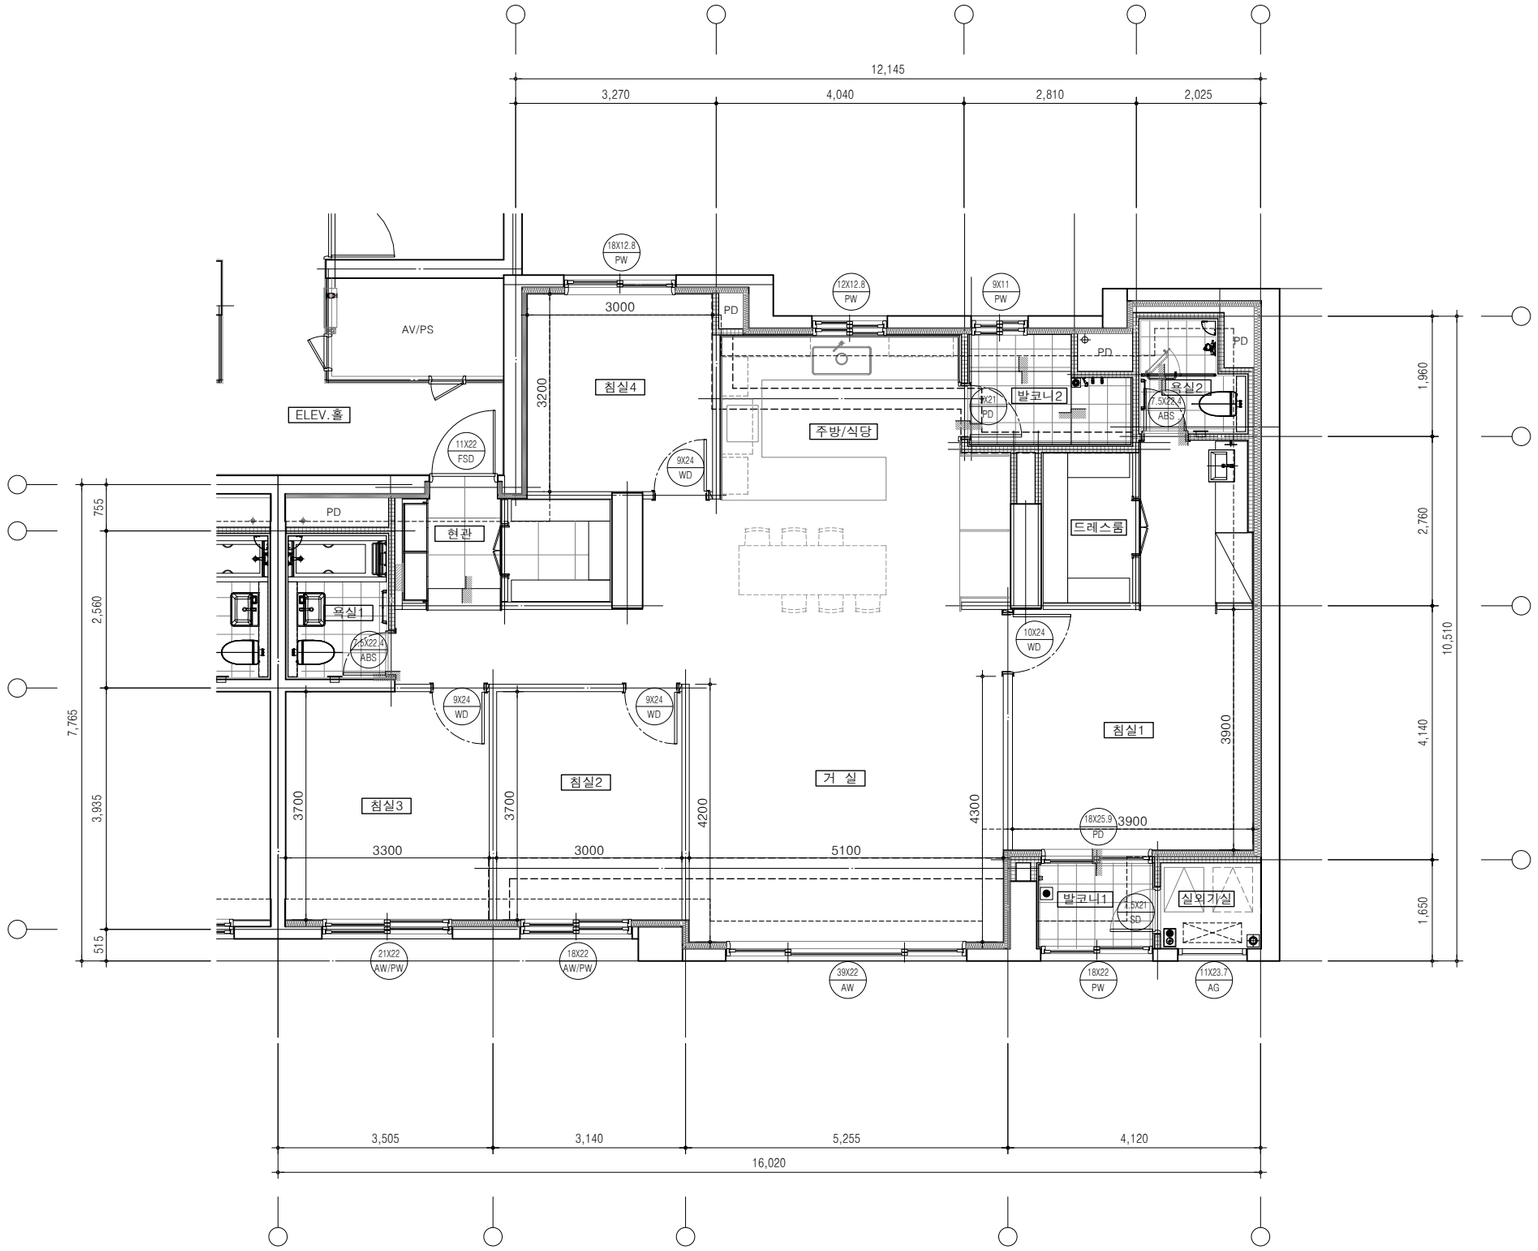

1 114A형 단위세대평면도(확장형)

축척 : 1/50

CLIENT

ARCHITECT

STRUCTURAL CONSULTANTS

NOTES

- 도면상의 치수는 참고 치수 이며, 실측시 결레받이 등의 시공으로 오차가 발생할 수 있음

REV.	DATE	DESCRIPTION	DRN	CHK	APP
4					
3					
2					
1					

PROJECT TITLE

NO.

DRAWING TITLE


114A형 단위세대평면도(확장형)

CHECKED BY/ DATE	APPROVED BY/ DATE
-	-
PROJECT ARCHITECT	PROJECT MANAGER
-	-
ENGINEER	DRAWN BY/ DATE
-	-

SCALE

A1: 1/50 A3: 1/100

DRAWING NO. A31-018 REV. 0

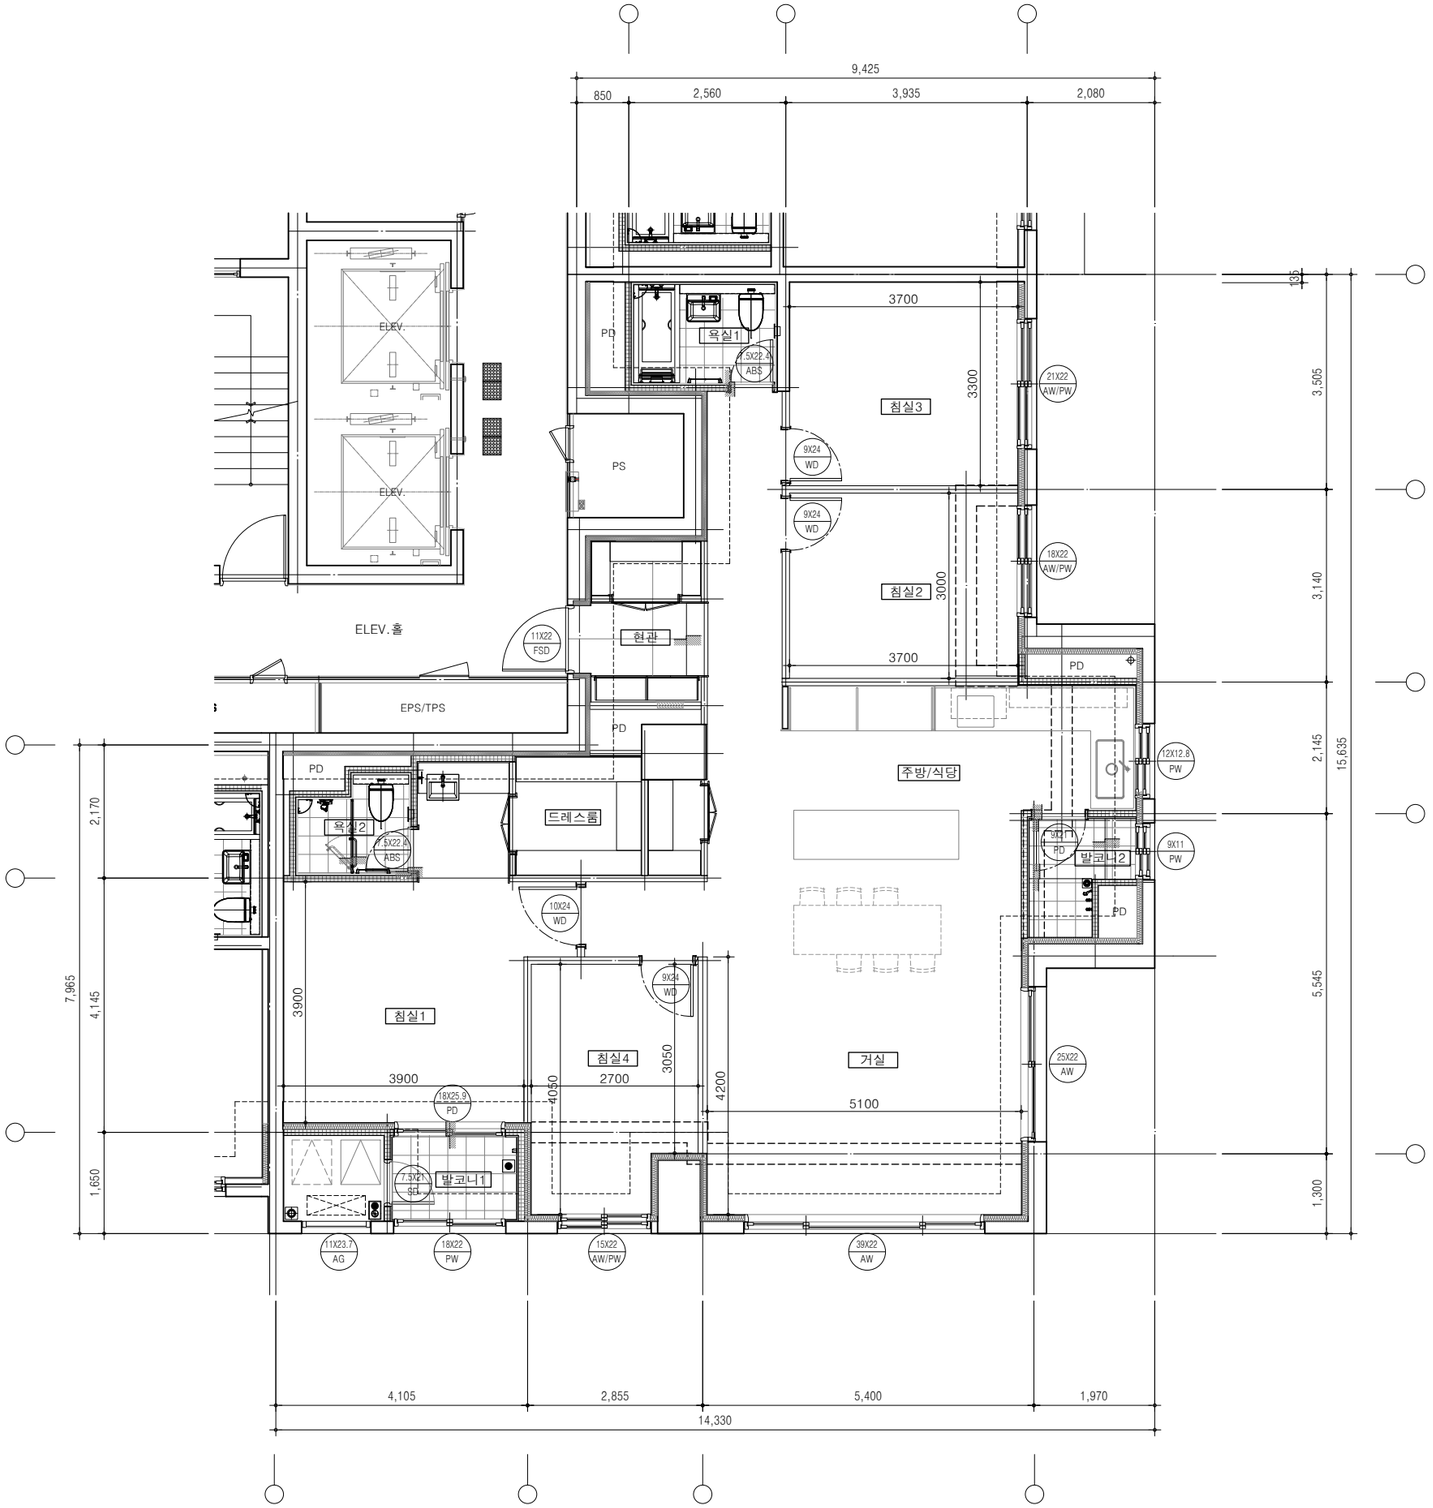

1 / _ 114B형 단위세대평면도(확장형)

축척 : 1/50

CLIENT

ARCHITECT

STRUCTURAL CONSULTANTS

NOTES

- 도면상의 치수는 참고 치수 이며, 실측시 결례분이 등의 시공으로 오차가 발생할 수 있음

REV.	DATE	DESCRIPTION	DRN	CHK	APP
4					
3					
2					
1					

PROJECT TITLE

NO.

DRAWING TITLE


114B형 단위세대평면도(확장형)

CHECKED BY/ DATE	APPROVED BY/ DATE
–	–
PROJECT ARCHITECT	PROJECT MANAGER
–	–
ENGINEER	DRAWN BY/ DATE
–	–

SCALE

A1: 1/50 A3: 1/100

DRAWING NO. A31-020 REV. 0

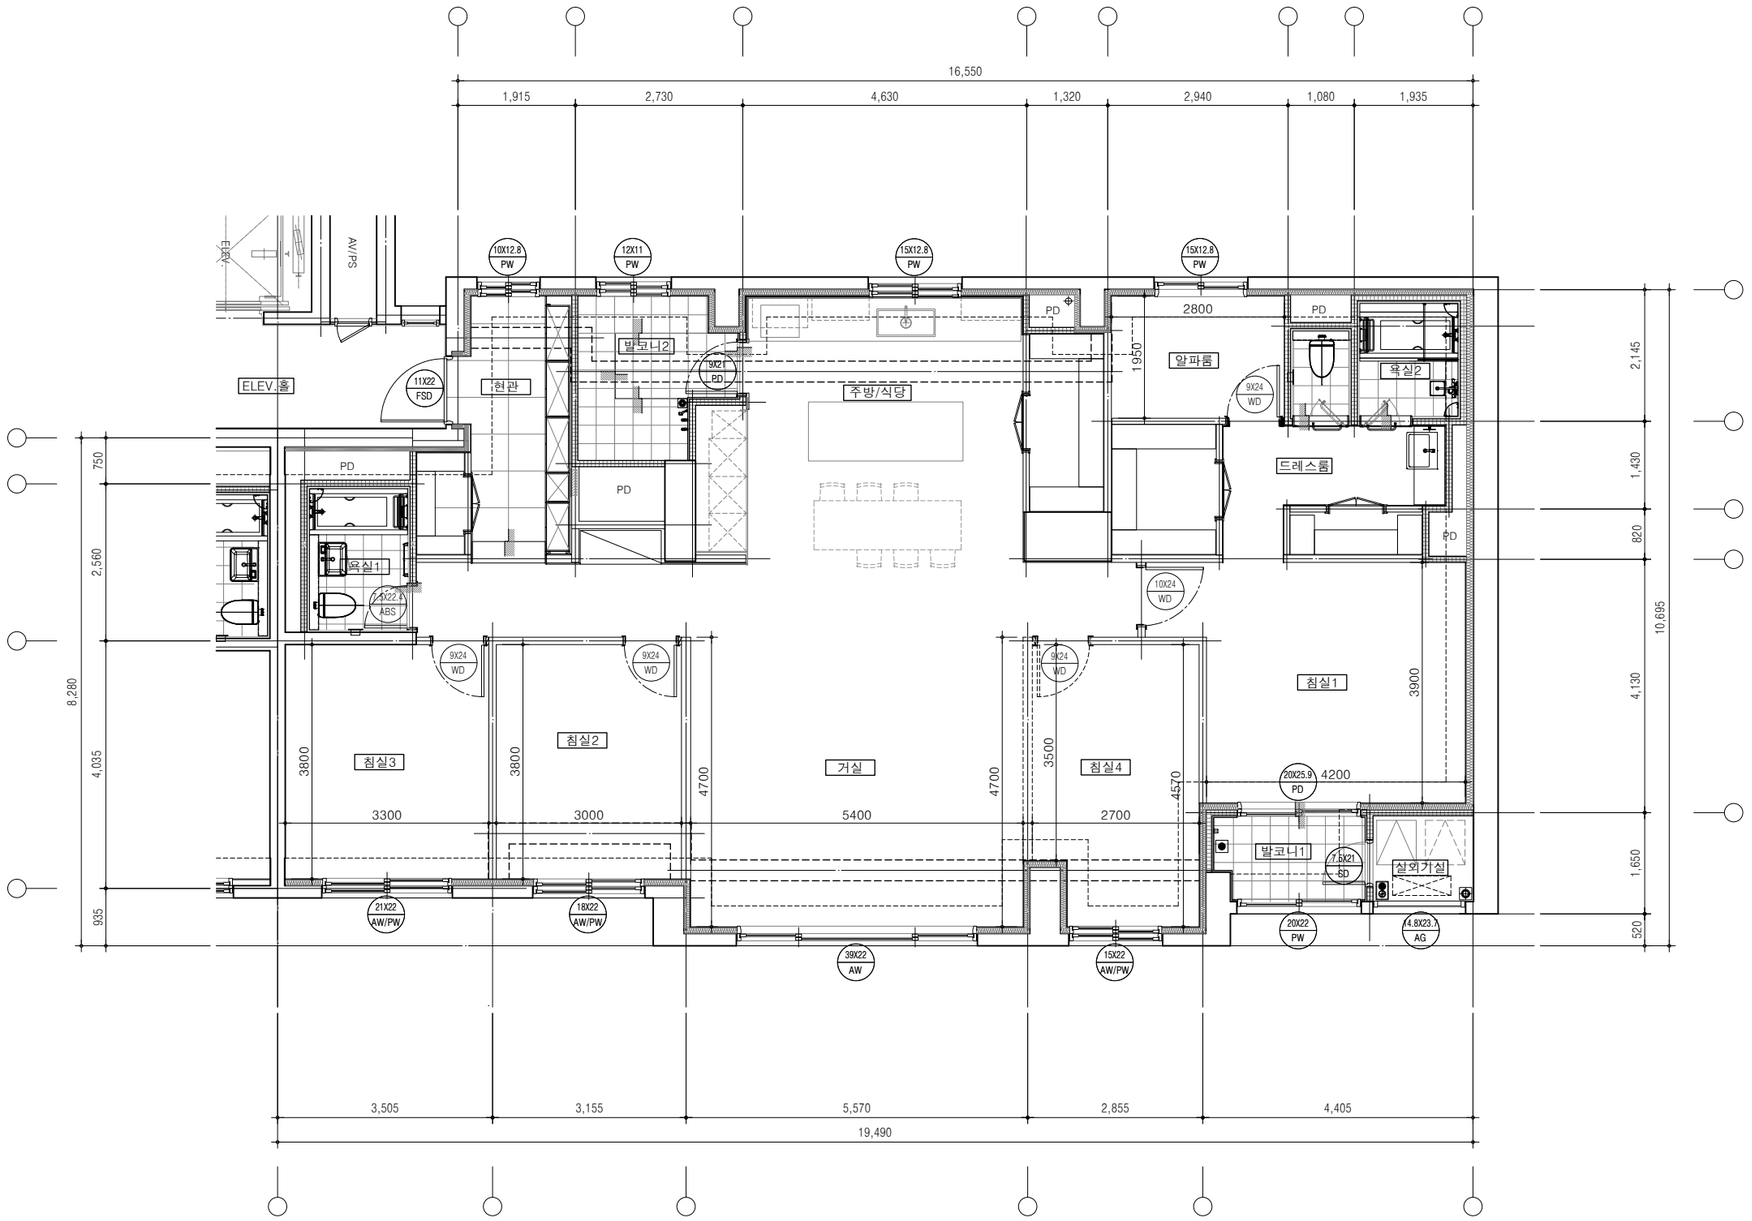

1 — 143형 단위세대평면도(확장형)

축척 : 1/50

CLIENT

ARCHITECT

STRUCTURAL CONSULTANTS

NOTES

- 도면상의 치수는 참고 치수 이며, 실측시 결레받이 등의 시공으로 오차가 발생할 수 있음

REV.	DATE	DESCRIPTION	DRN	CHK	APP
4					
3					
2					
1					

PROJECT TITLE

NO.

DRAWING TITLE

143형 단위세대평면도(확장형)


CHECKED BY/ DATE	APPROVED BY/ DATE
–	–
PROJECT ARCHITECT	PROJECT MANAGER
–	–
ENGINEER	DRAWN BY/ DATE
–	–

SCALE

A1 : 1/50 A3 : 1/100

DRAWING NO. A31-022

REV. 0

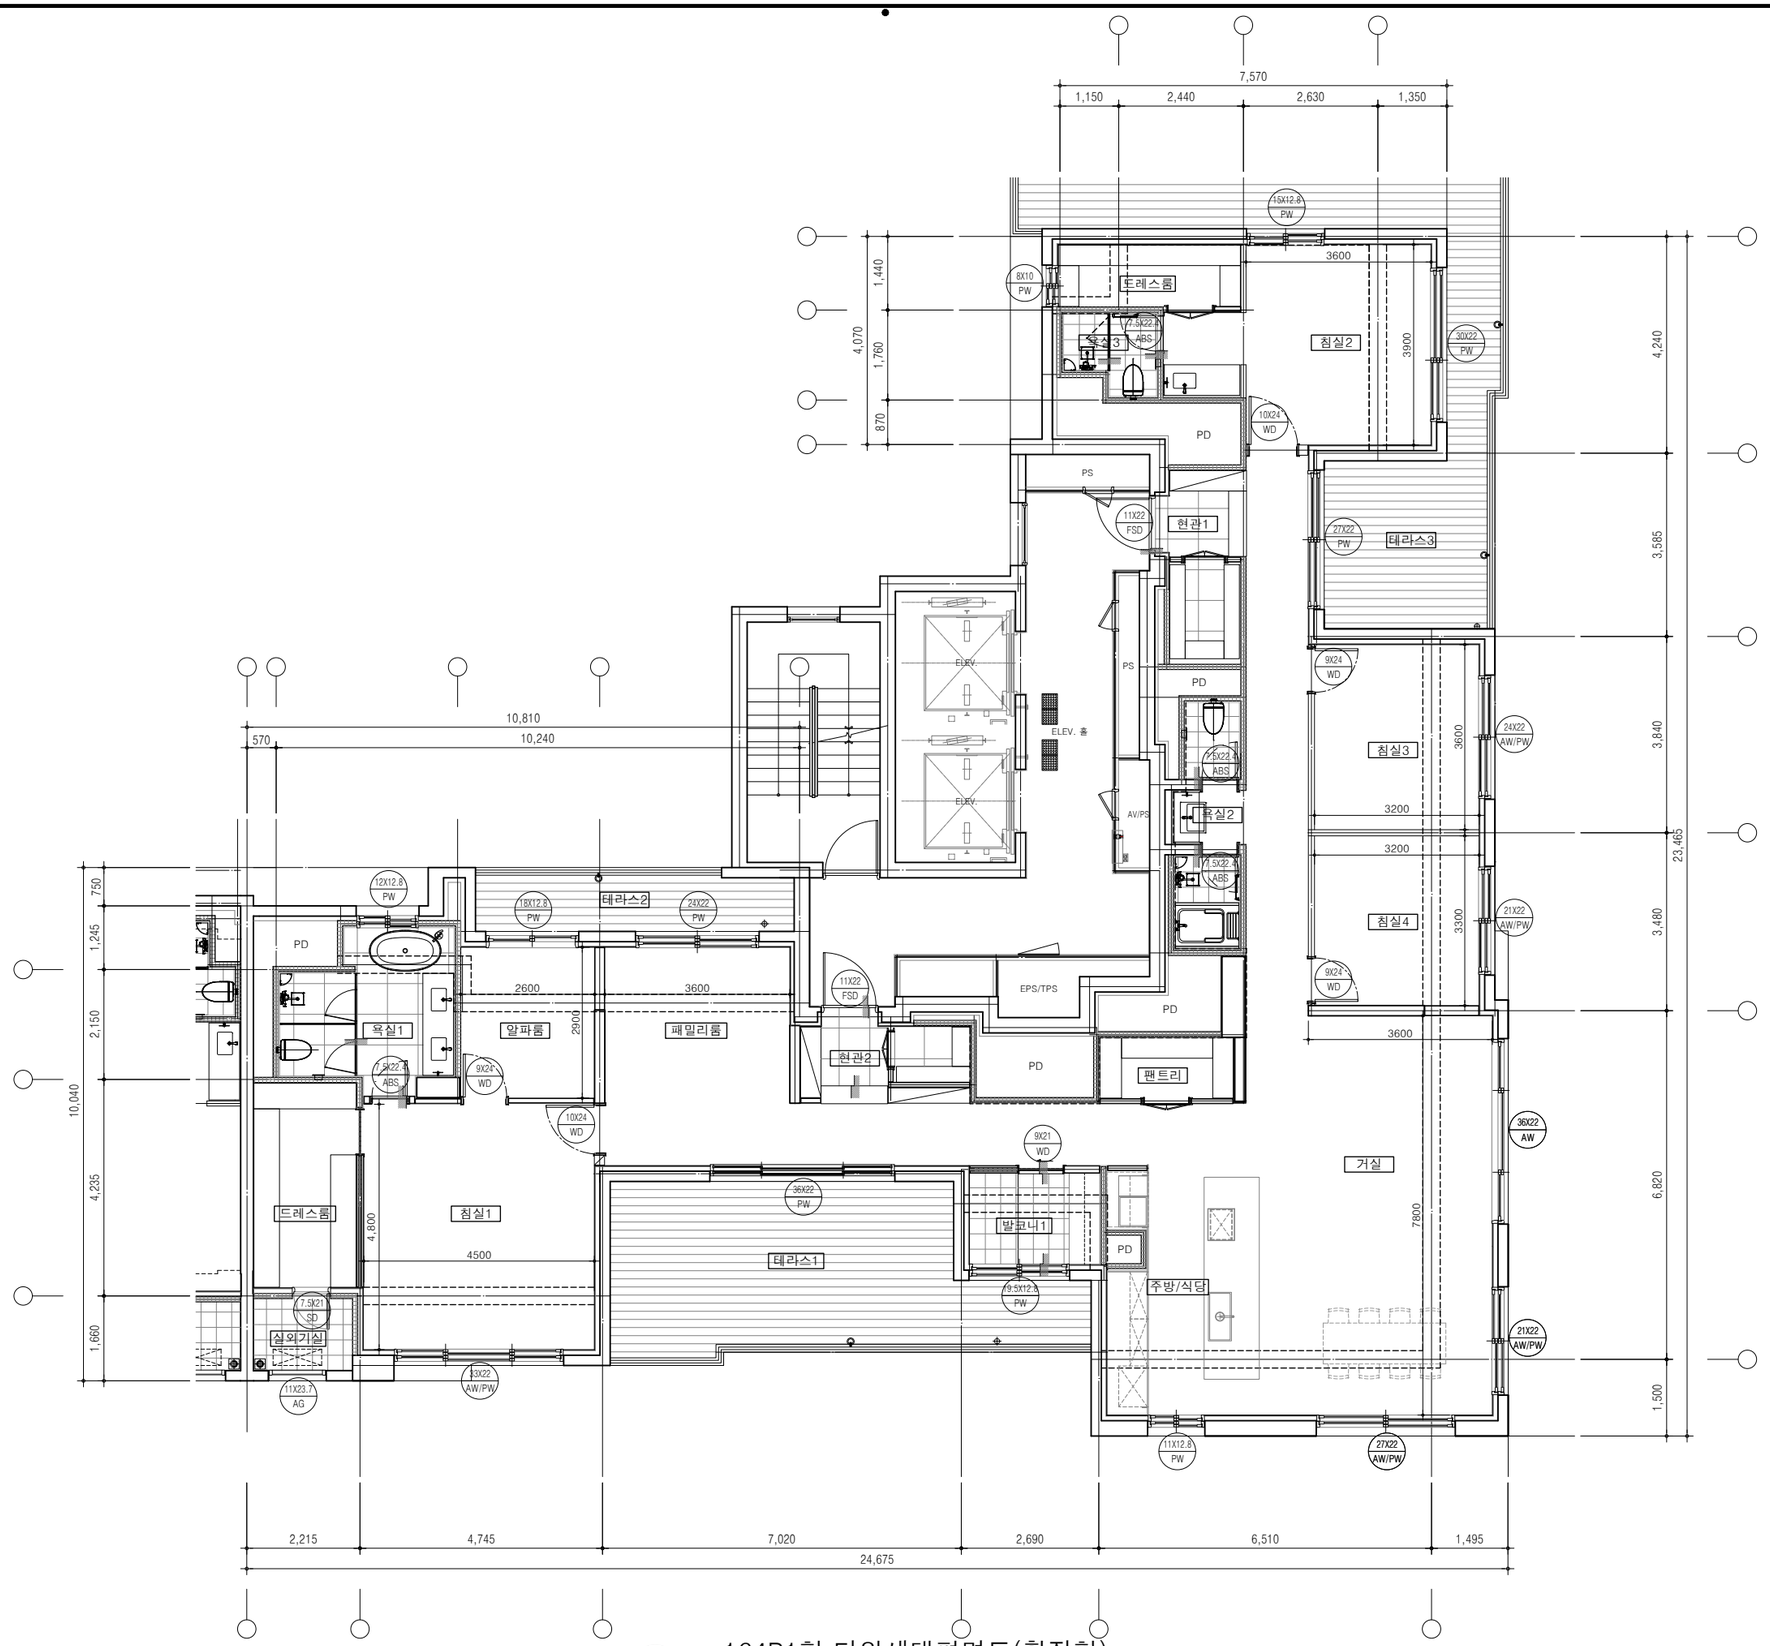

1 — 164P1형 단위세대평면도(확장형)

축척 : 1/60

CLIENT

ARCHITECT

STRUCTURAL CONSULTANTS

NOTES

- 도면상의 치수는 참고 치수 이며, 실측시 결레받이 등의 시공으로 오차가 발생할 수 있음

REV.	DATE	DESCRIPTION	DRN	CHK	APP
4					
3					
2					
1					

PROJECT TITLE

NO.

DRAWING TITLE

164P1형 단위세대평면도(확장형)


CHECKED BY/ DATE	APPROVED BY/ DATE
–	–
PROJECT ARCHITECT	PROJECT MANAGER
–	–
ENGINEER	DRAWN BY/ DATE
–	–

SCALE

A1: 1/60 A3: 1/120

DRAWING NO. A31-024

REV. 0

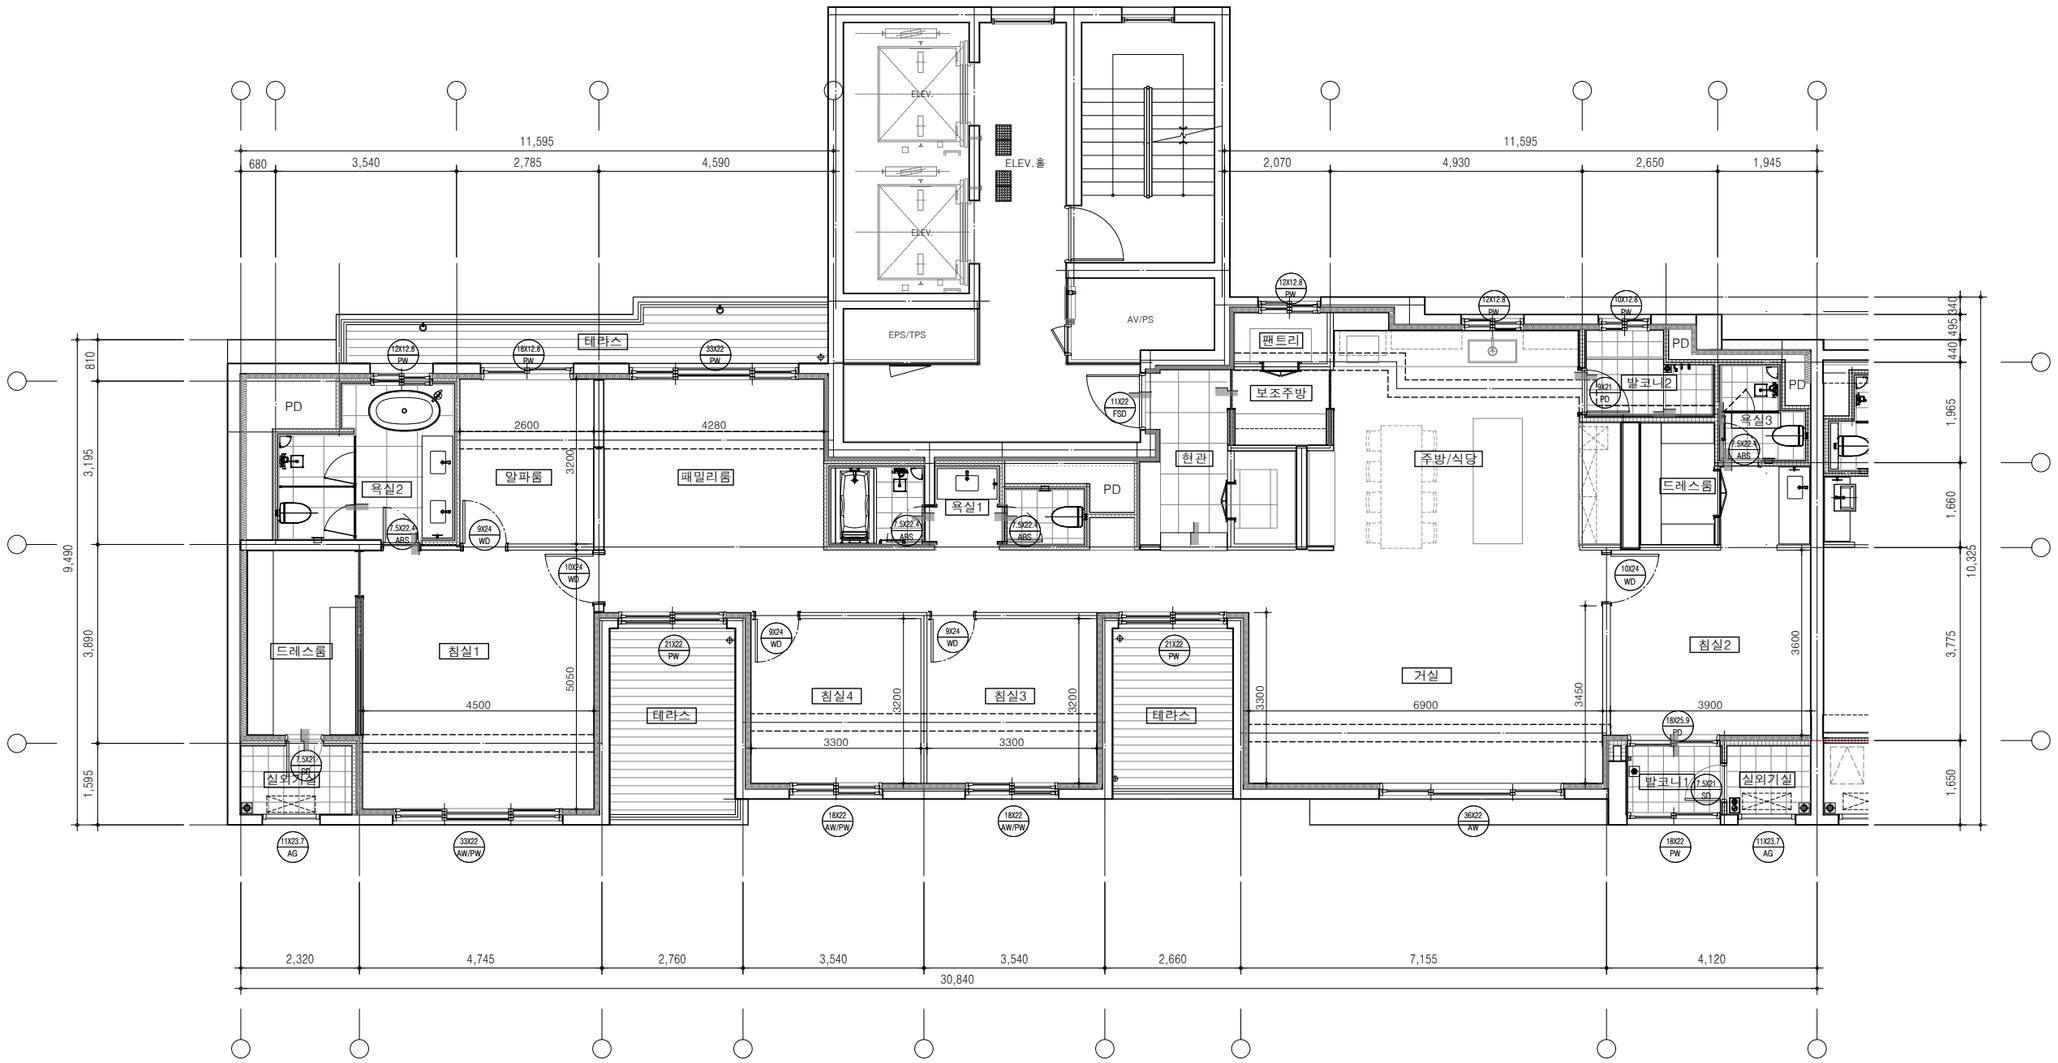

1 _ 164P2형 단위세대평면도(확장형)

축척 : 1/60

CLIENT

ARCHITECT

STRUCTURAL CONSULTANTS

NOTES

- 도면상의 치수는 참고 치수 이며, 실측시 결례분이 등의 시공으로 오차가 발생할 수 있음

REV.	DATE	DESCRIPTION	DRN	CHK	APP
4					
3					
2					
1					

PROJECT TITLE

NO.

DRAWING TITLE

164P2형 단위세대평면도(확장형)

CHECKED BY/ DATE	APPROVED BY/ DATE
-	-
PROJECT ARCHITECT	PROJECT MANAGER
-	-
ENGINEER	DRAWN BY/ DATE
-	-

SCALE

A1: 1/60 A3: 1/120

DRAWING NO. A31-026 REV. 0



1 / – 164P3형 단위세대평면도(확장형)

축척 : 1/60

타입	구 분	
164 P3형	세대수	2세대
	전용면적	164.99㎡
	주거공용면적	49.05㎡
	공급면적	214.04㎡
	기타공용면적	150.56㎡
	계약면적	364.60㎡

CLIENT

ARCHITECT

STRUCTURAL CONSULTANTS

NOTES

- 도면상의 치수는 참고 치수 이며, 실측시 결레받이 등의 시공으로 오차가 발생할 수 있음

REV.	DATE	DESCRIPTION	DRN	CHK	APP
4					
3					
2					
1					

PROJECT TITLE

NO.

DRAWING TITLE


164P3형 단위세대평면도(확장형)

CHECKED BY/ DATE	APPROVED BY/ DATE
–	–
PROJECT ARCHITECT	PROJECT MANAGER
–	–
ENGINEER	DRAWN BY/ DATE
–	–

SCALE

A1: 1/60 A3: 1/120

DRAWING NO. A31-028 REV. 0

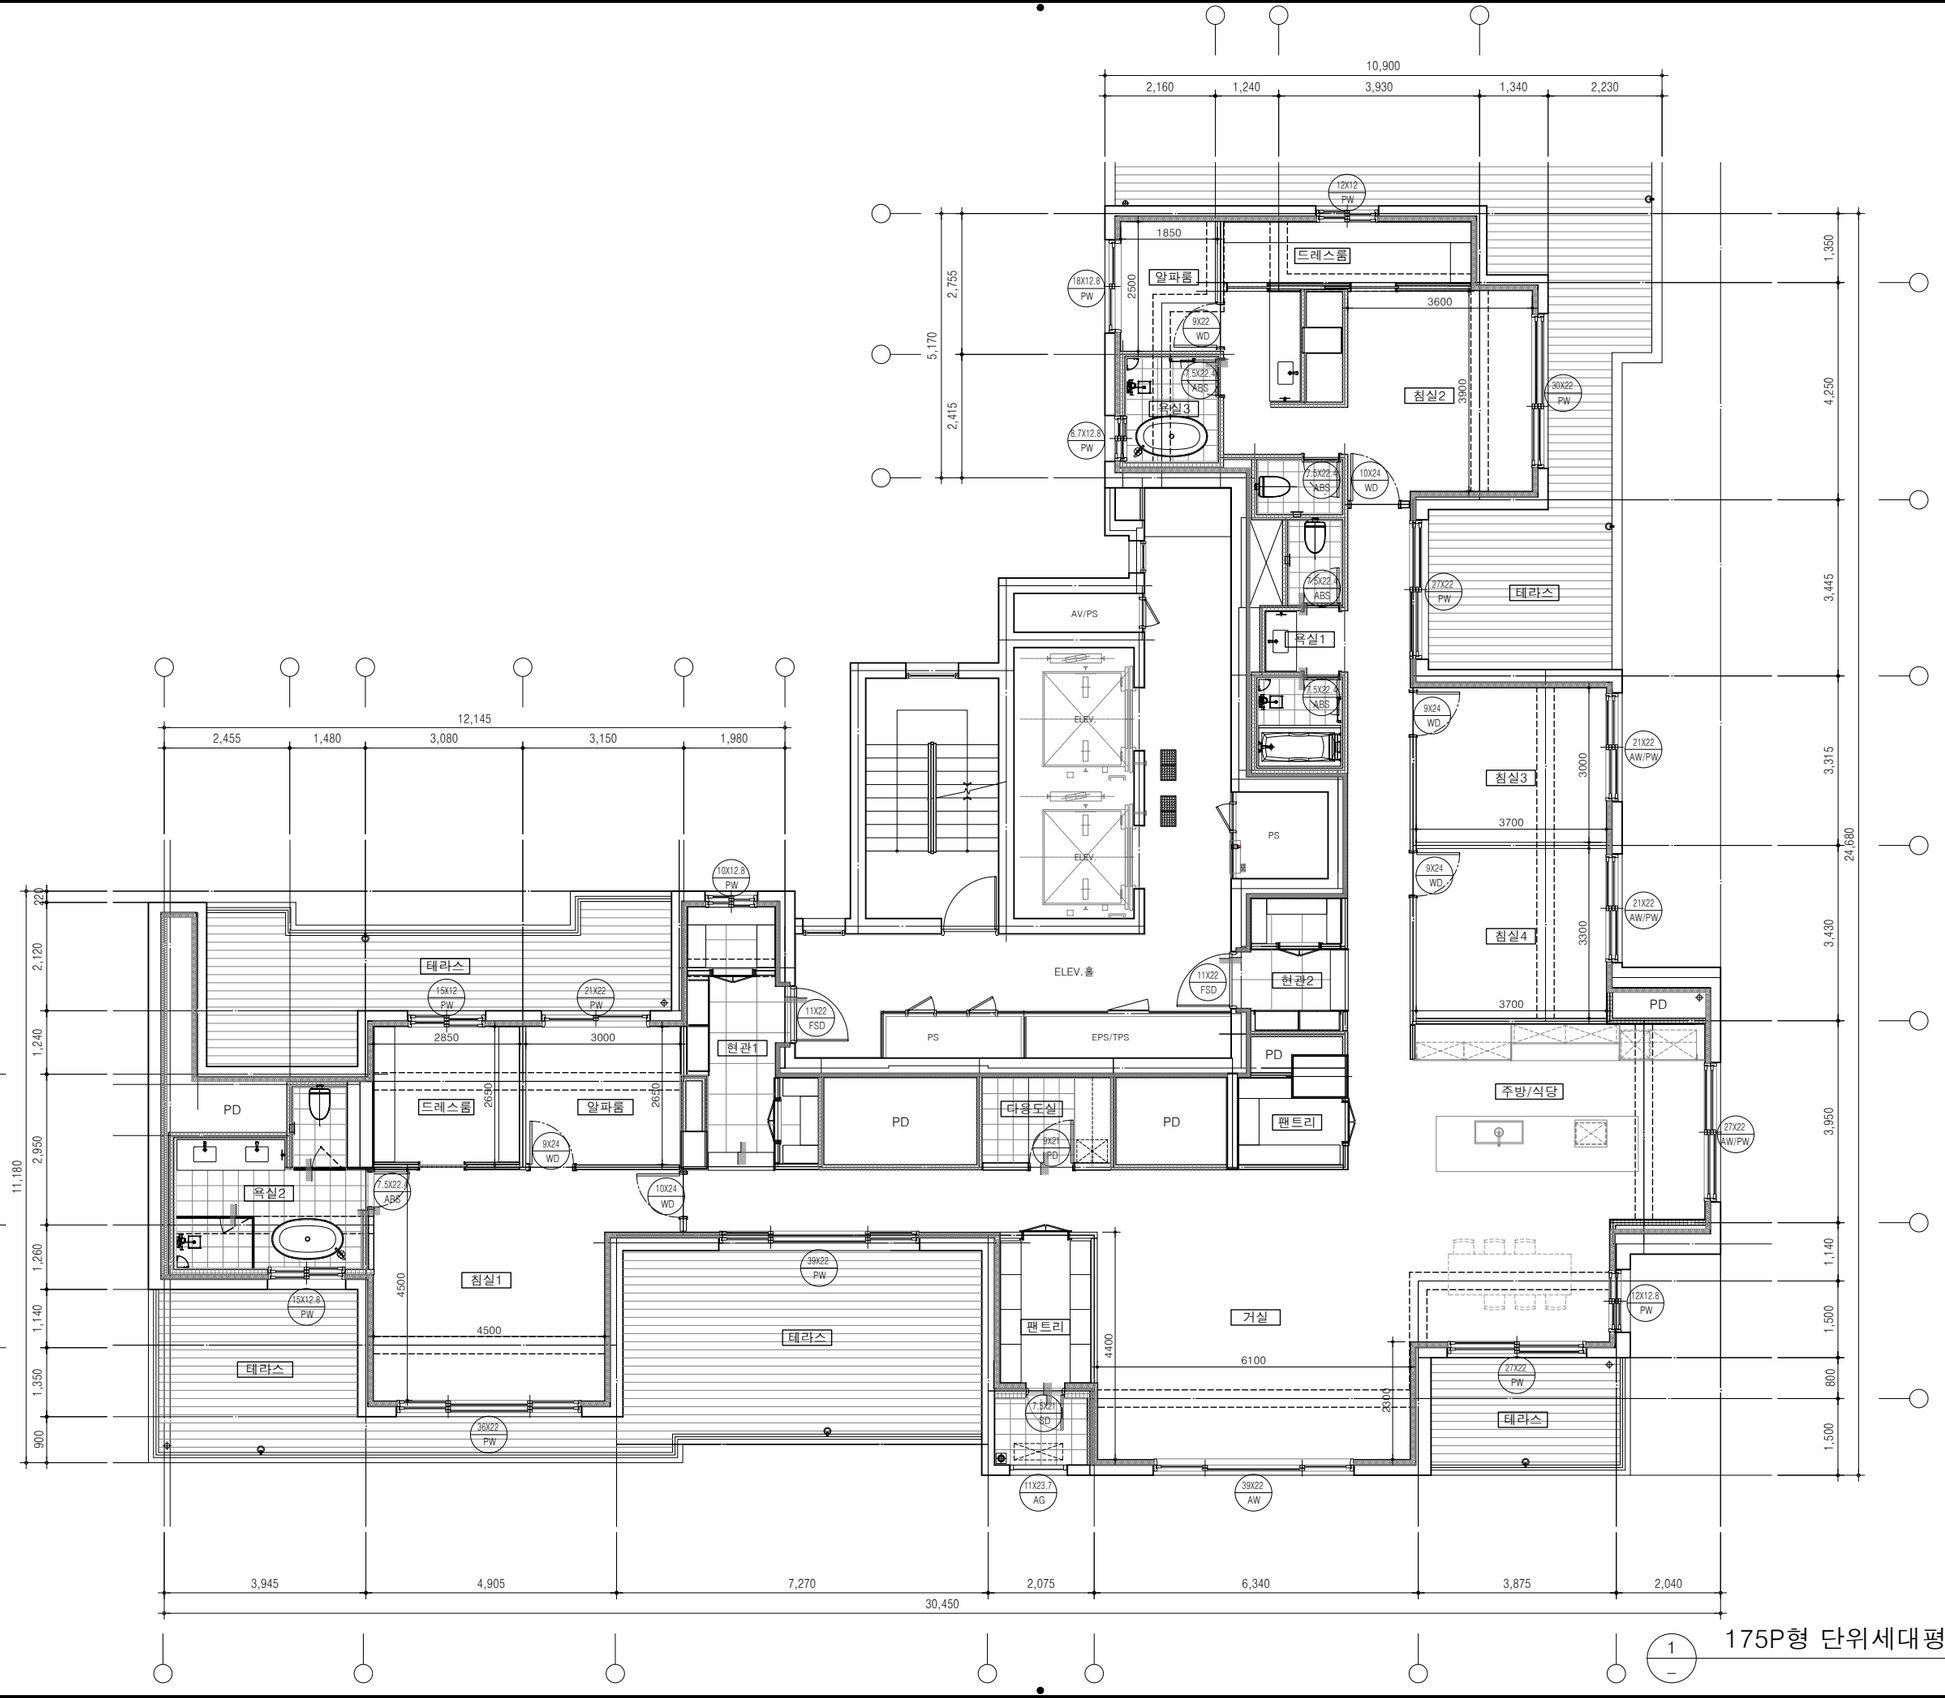

1 / –

175P형 단위세대평면도(확장형)

축척 : 1/60

CLIENT

ARCHITECT

STRUCTURAL CONSULTANTS

NOTES

- 도면상의 치수는 참고 치수 이며, 실측시 걸레받이 등의 시공으로 오차가 발생할 수 있음

REV.	DATE	DESCRIPTION	DRN	CHK	APP
4					
3					
2					
1					

PROJECT TITLE

NO.

DRAWING TITLE

175P형 단위세대평면도(확장형)

CHECKED BY/ DATE	APPROVED BY/ DATE
–	–
PROJECT ARCHITECT	PROJECT MANAGER
–	–
ENGINEER	DRAWN BY/ DATE
–	–

SCALE

A1: 1/60 A3: 1/120

DRAWING NO. A31-030

REV. 0